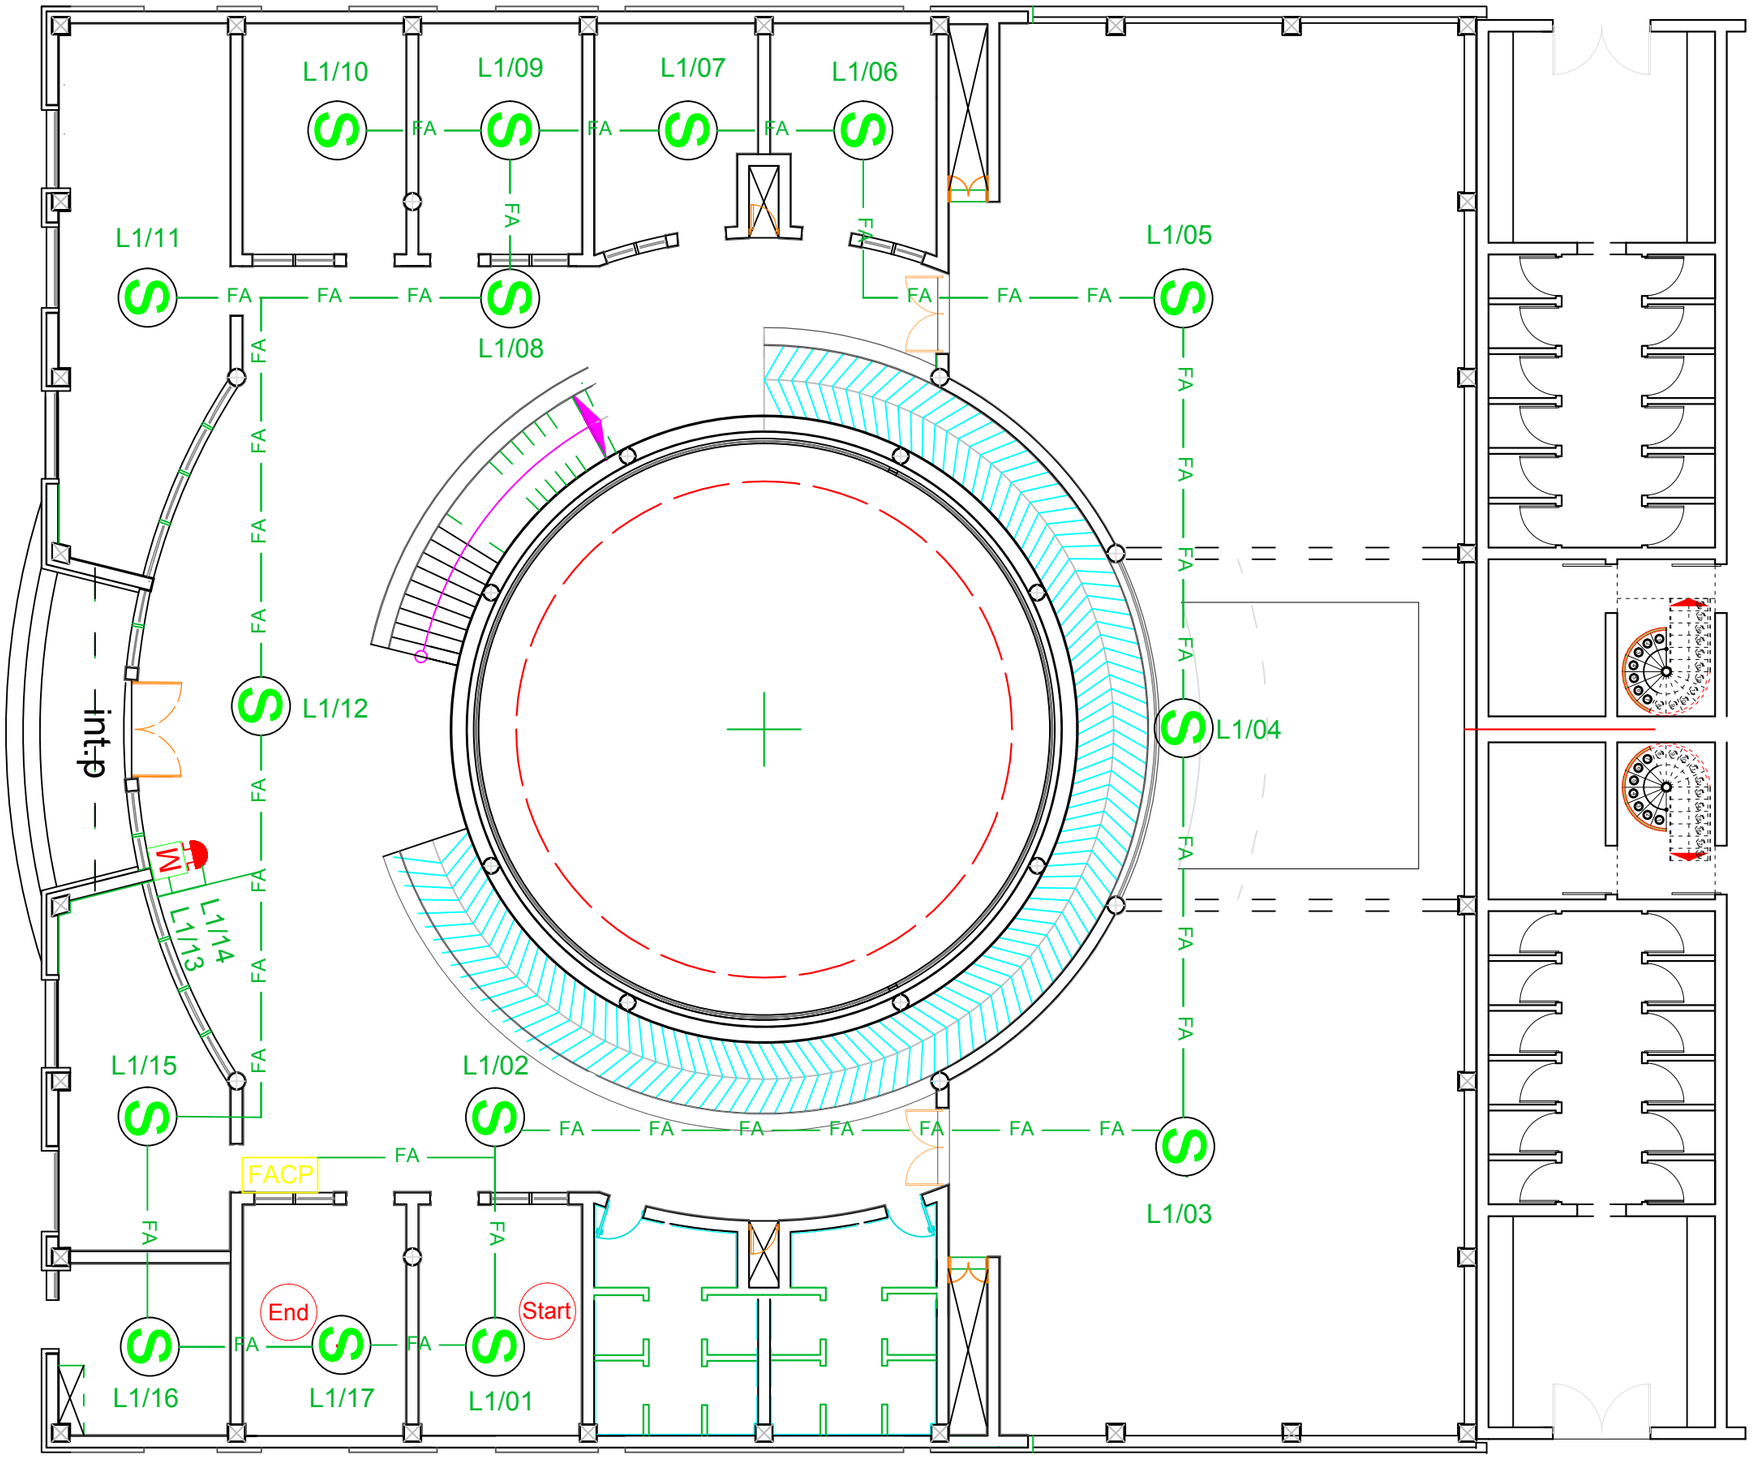

Legend :

Symbol	Description	NO
S	Ceiling Smoke Detector	15
	Flash+Sounder	1
M	Break Glass	1
FACP	Fire Alarm Contro Panel	
Loop 1 : k1 - G (1- 17)		

ديوان الوقف الشيعي
العتبة العباسية المقدسة
قسم المشاريع الهندسية

اسم المشروع :
مدارس العميد
الحـــر

رسم المهندس :
أحمد قصي

التدقيق الشبكي المهندس :
محمد رعد

تصميم المهندس :
حيدر حميد

تدقيق المهندس :
فراس عباس

مصادقة المهندس :
ضياء مجيد الصـائغ

اسم المخطط :
منظومة
اطفاء الحريق

عنوان المخطط :
مخططات بناية الروضـــة ١
الطابق الارضي

Layout No.	26
Revision	2
Date	21/08/2022
Draw Scale	1\1

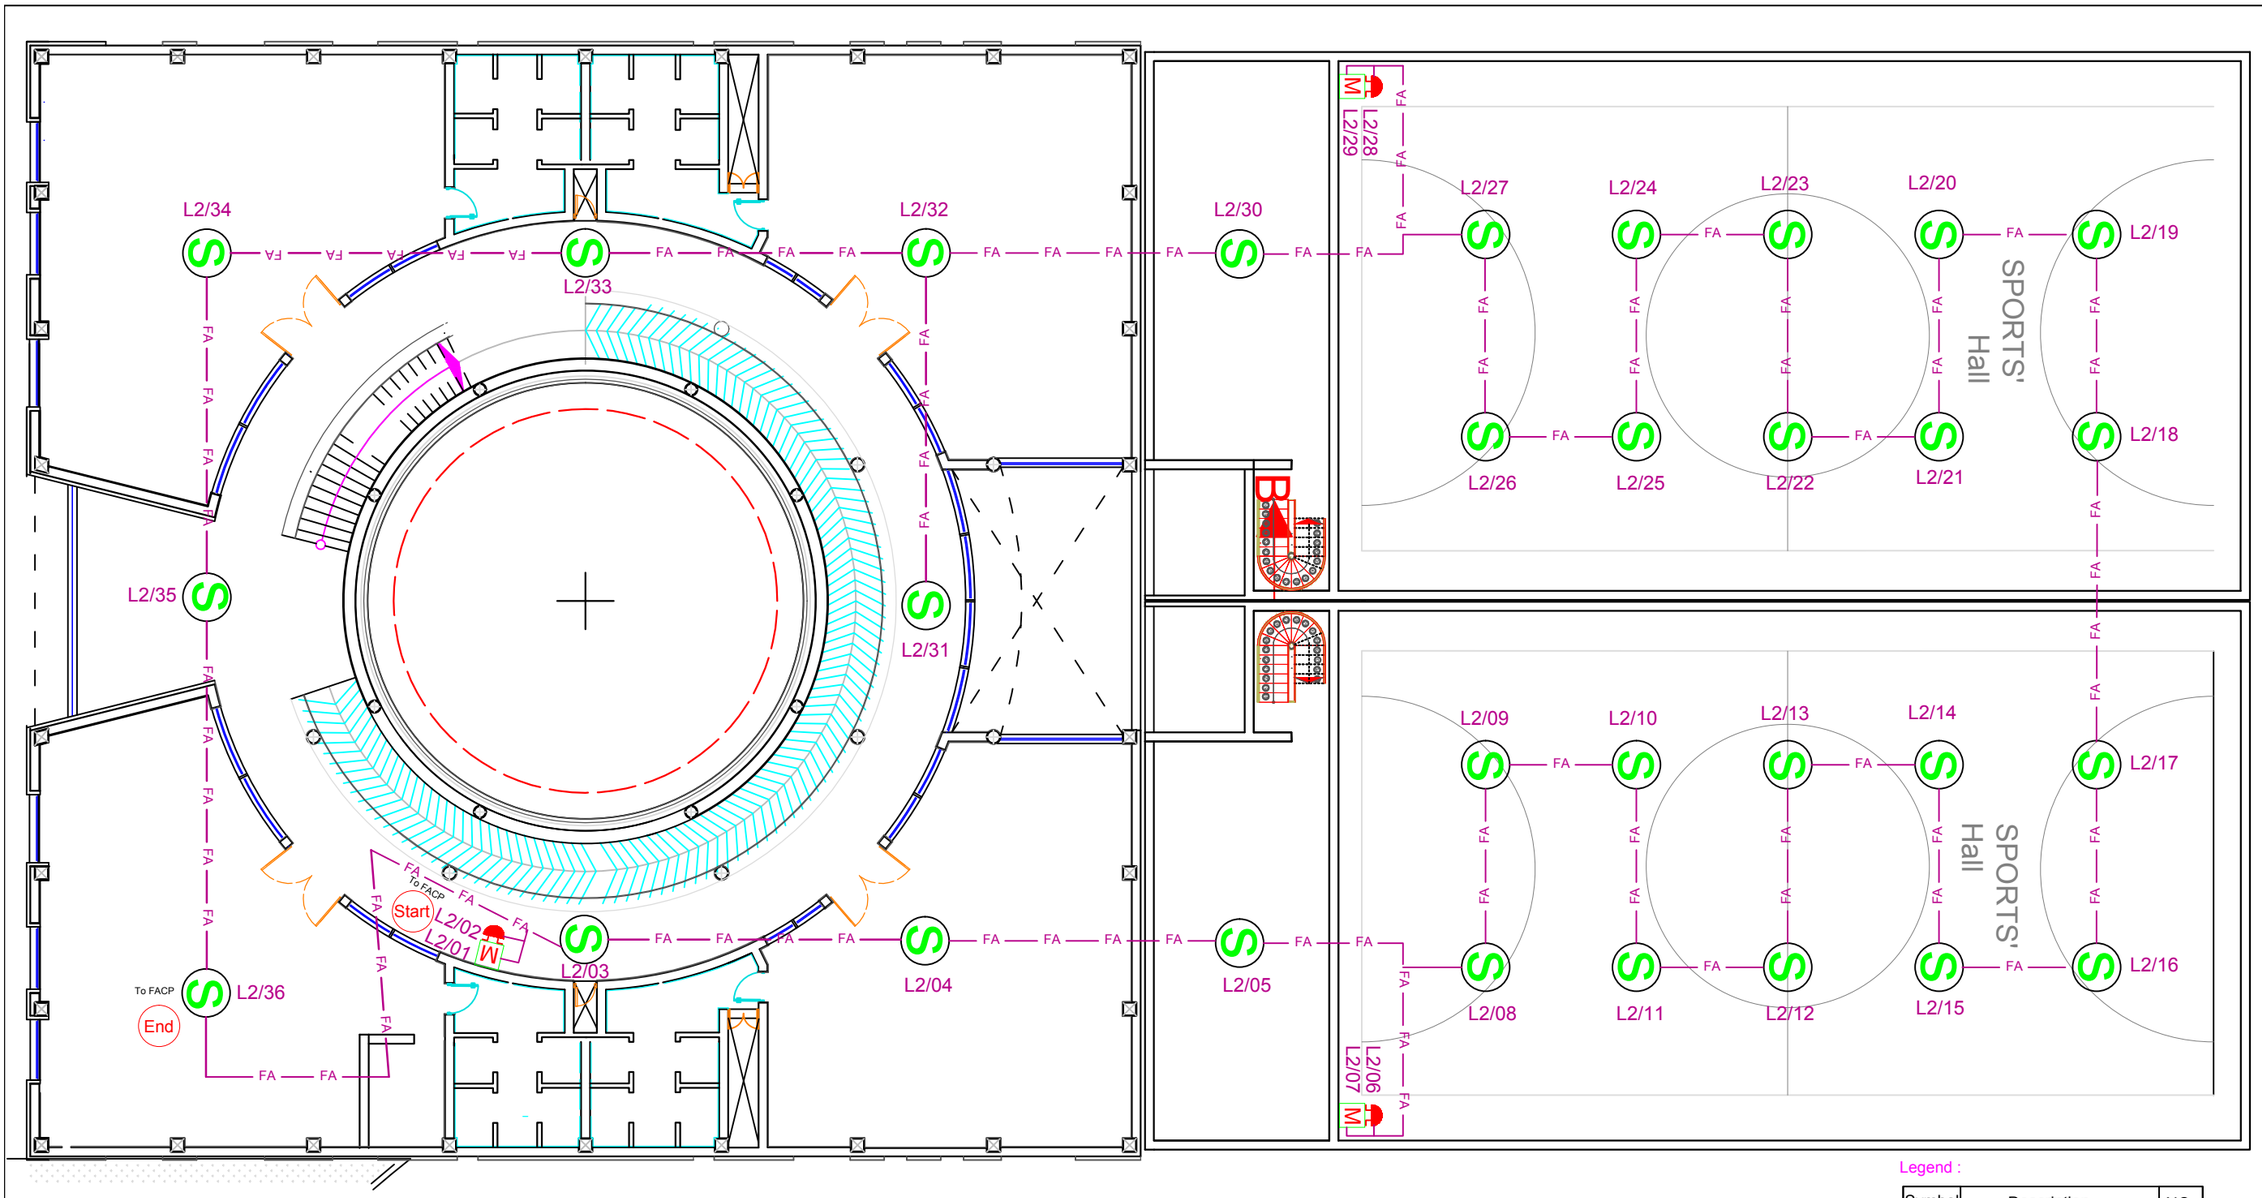

Legend :

Symbol	Description	NO
S	Ceiling Smoke Detector	27
	Flash+Sounder	3
M	Break Glass	3
FACP	Fire Alarm Contro Panel	
Loop 2 : k1 - F1 (1- 36)		

ديوان الوقف الشيعي
العتبة العباسية المقدسة
قسم المشاريع الهندسية

اسم المشروع :
مدارس العميد
الحـــر

رسم المهندس :
أحمد قصي

التدقيق الشبكي المهندس :
محمد رعد

تصميم المهندس :
حيدر حميد

تدقيق المهندس :
فراس عباس

مصادقة المهندس :
ضياء مجيد الصائغ

اسم المخطط :
منظومة
اطفاء الحريق

عنوان المخطط :
مخططات بناية الروضـة ١
الطابق الأول

Layout No.	27
Revision	2
Date	21/08/2022
Draw Scale	1\1

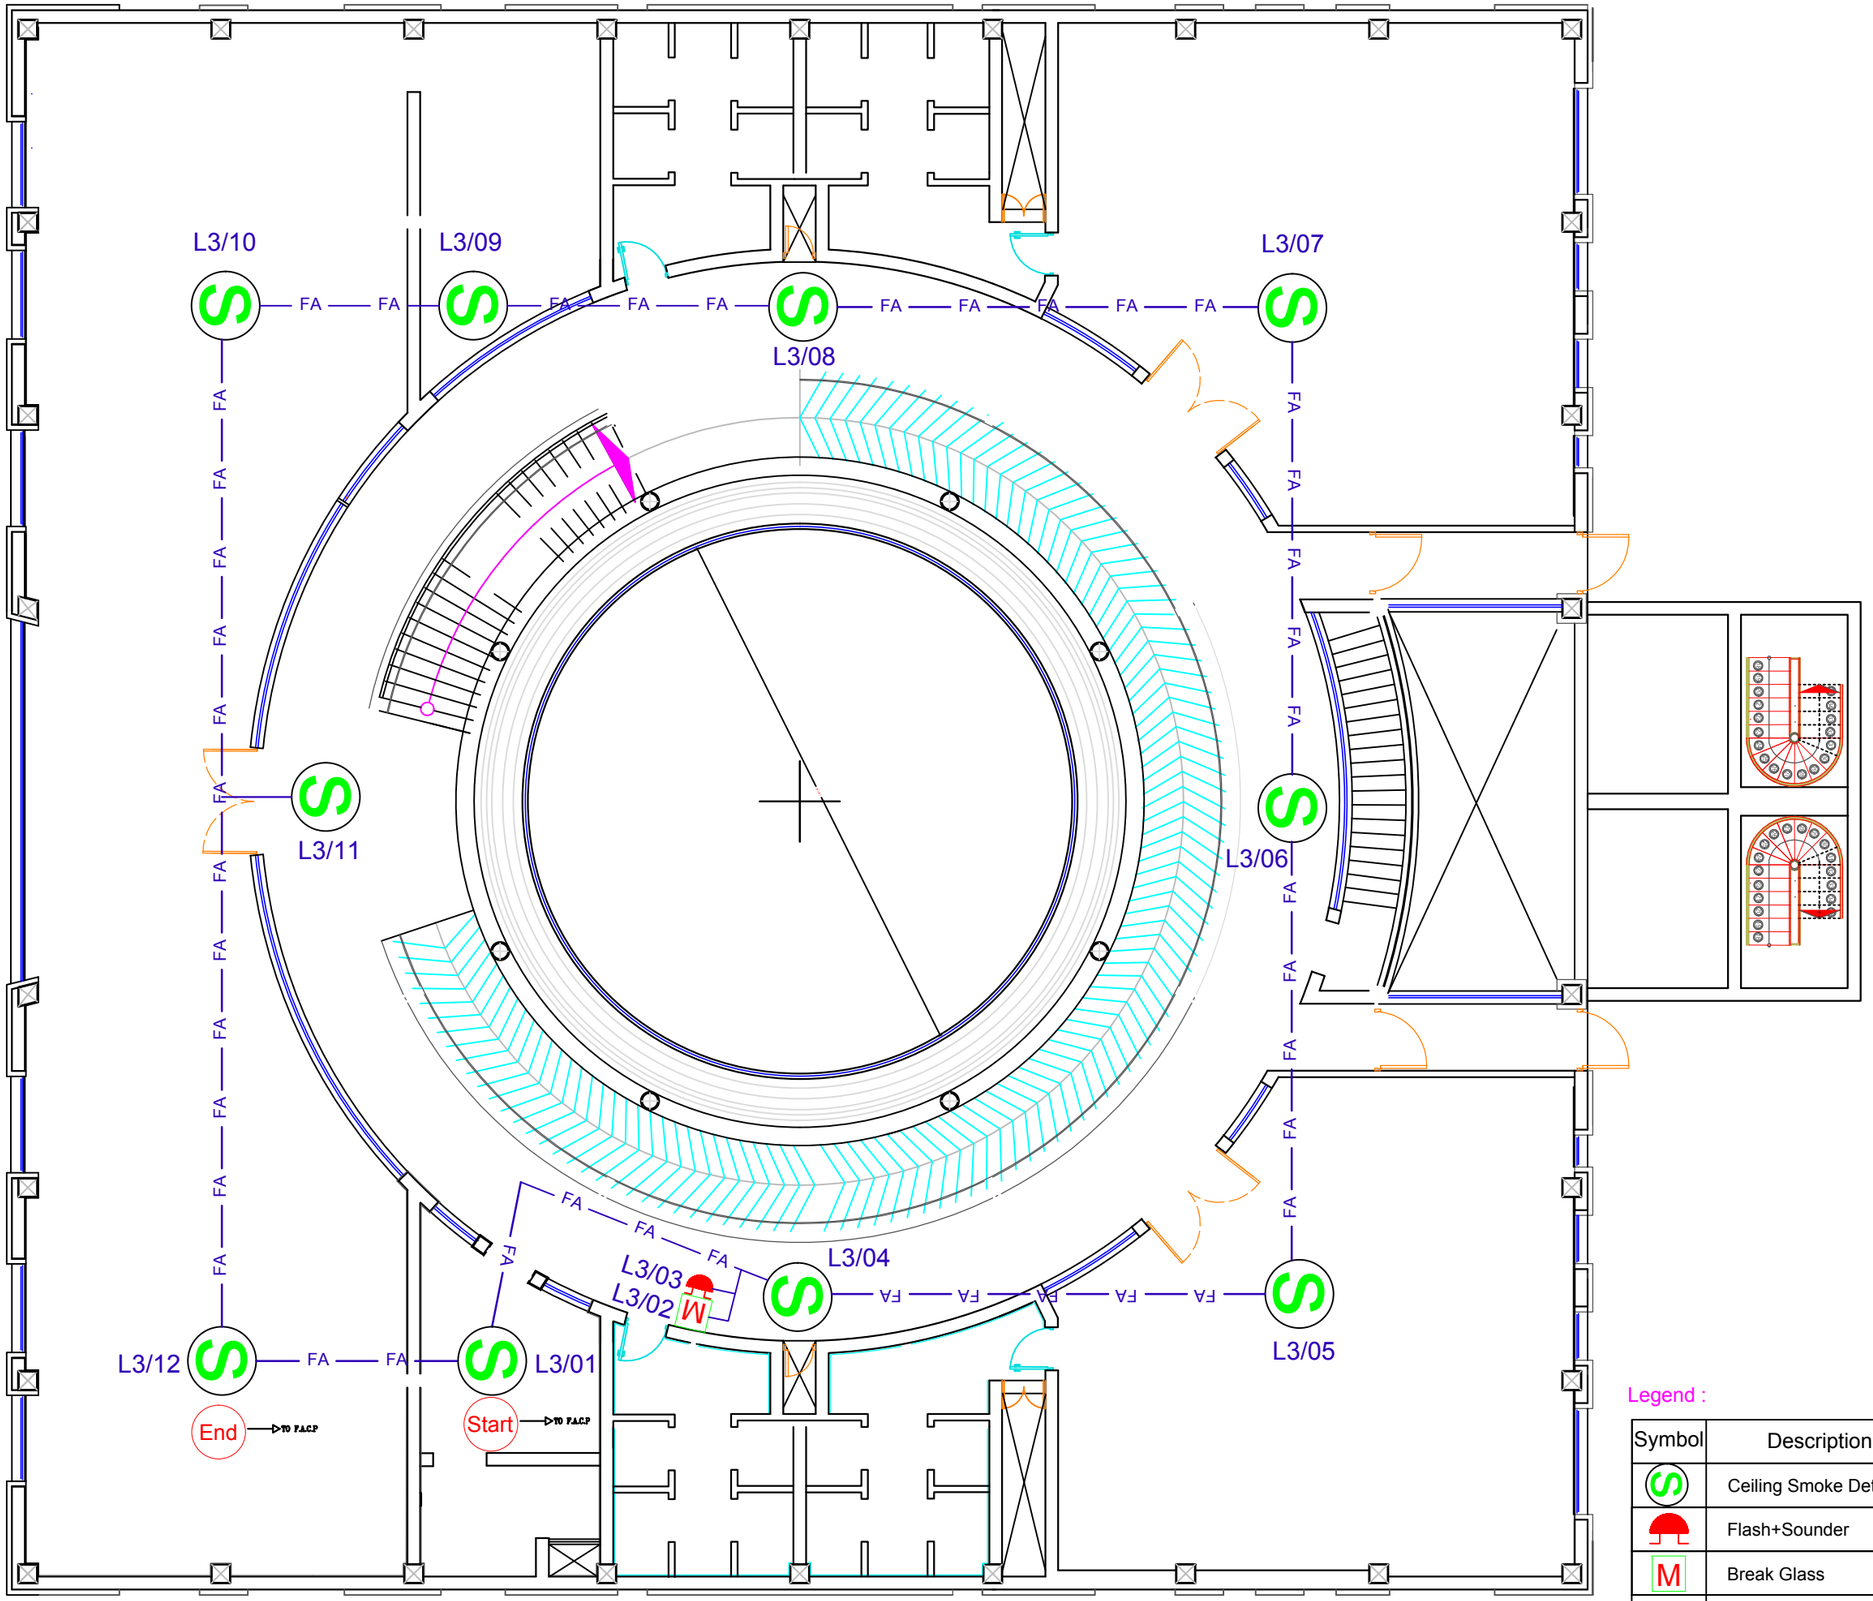

Legend :

Symbol	Description	NO
S	Ceiling Smoke Detector	10
	Flash+Sounder	1
M	Break Glass	1
FACP	Fire Alarm Contro Panel	
	Loop 3 : k1 - F2 (1- 12)	

ديوان الوقف الشيعي
العتبة العباسية المقدسة
قسم المشاريع الهندسية

اسم المشروع :
مدارس العميد
الحـــر

رسم المهندس :
أحمد قصي

التدقيق الشبكي المهندس :
محمد رعد

تصميم المهندس :
حيدر حميد

تدقيق المهندس :
فراس عباس

مصادقة المهندس :
ضياء مجيد الصـائغ

اسم المخطط :
منظومة
اطفاء الحريق

عنوان المخطط :
مخططات بناية الروضـــة ١
الطابق الثاني

Layout No.	28
Revision	2
Date	21/08/2022
Draw Scale	1\1

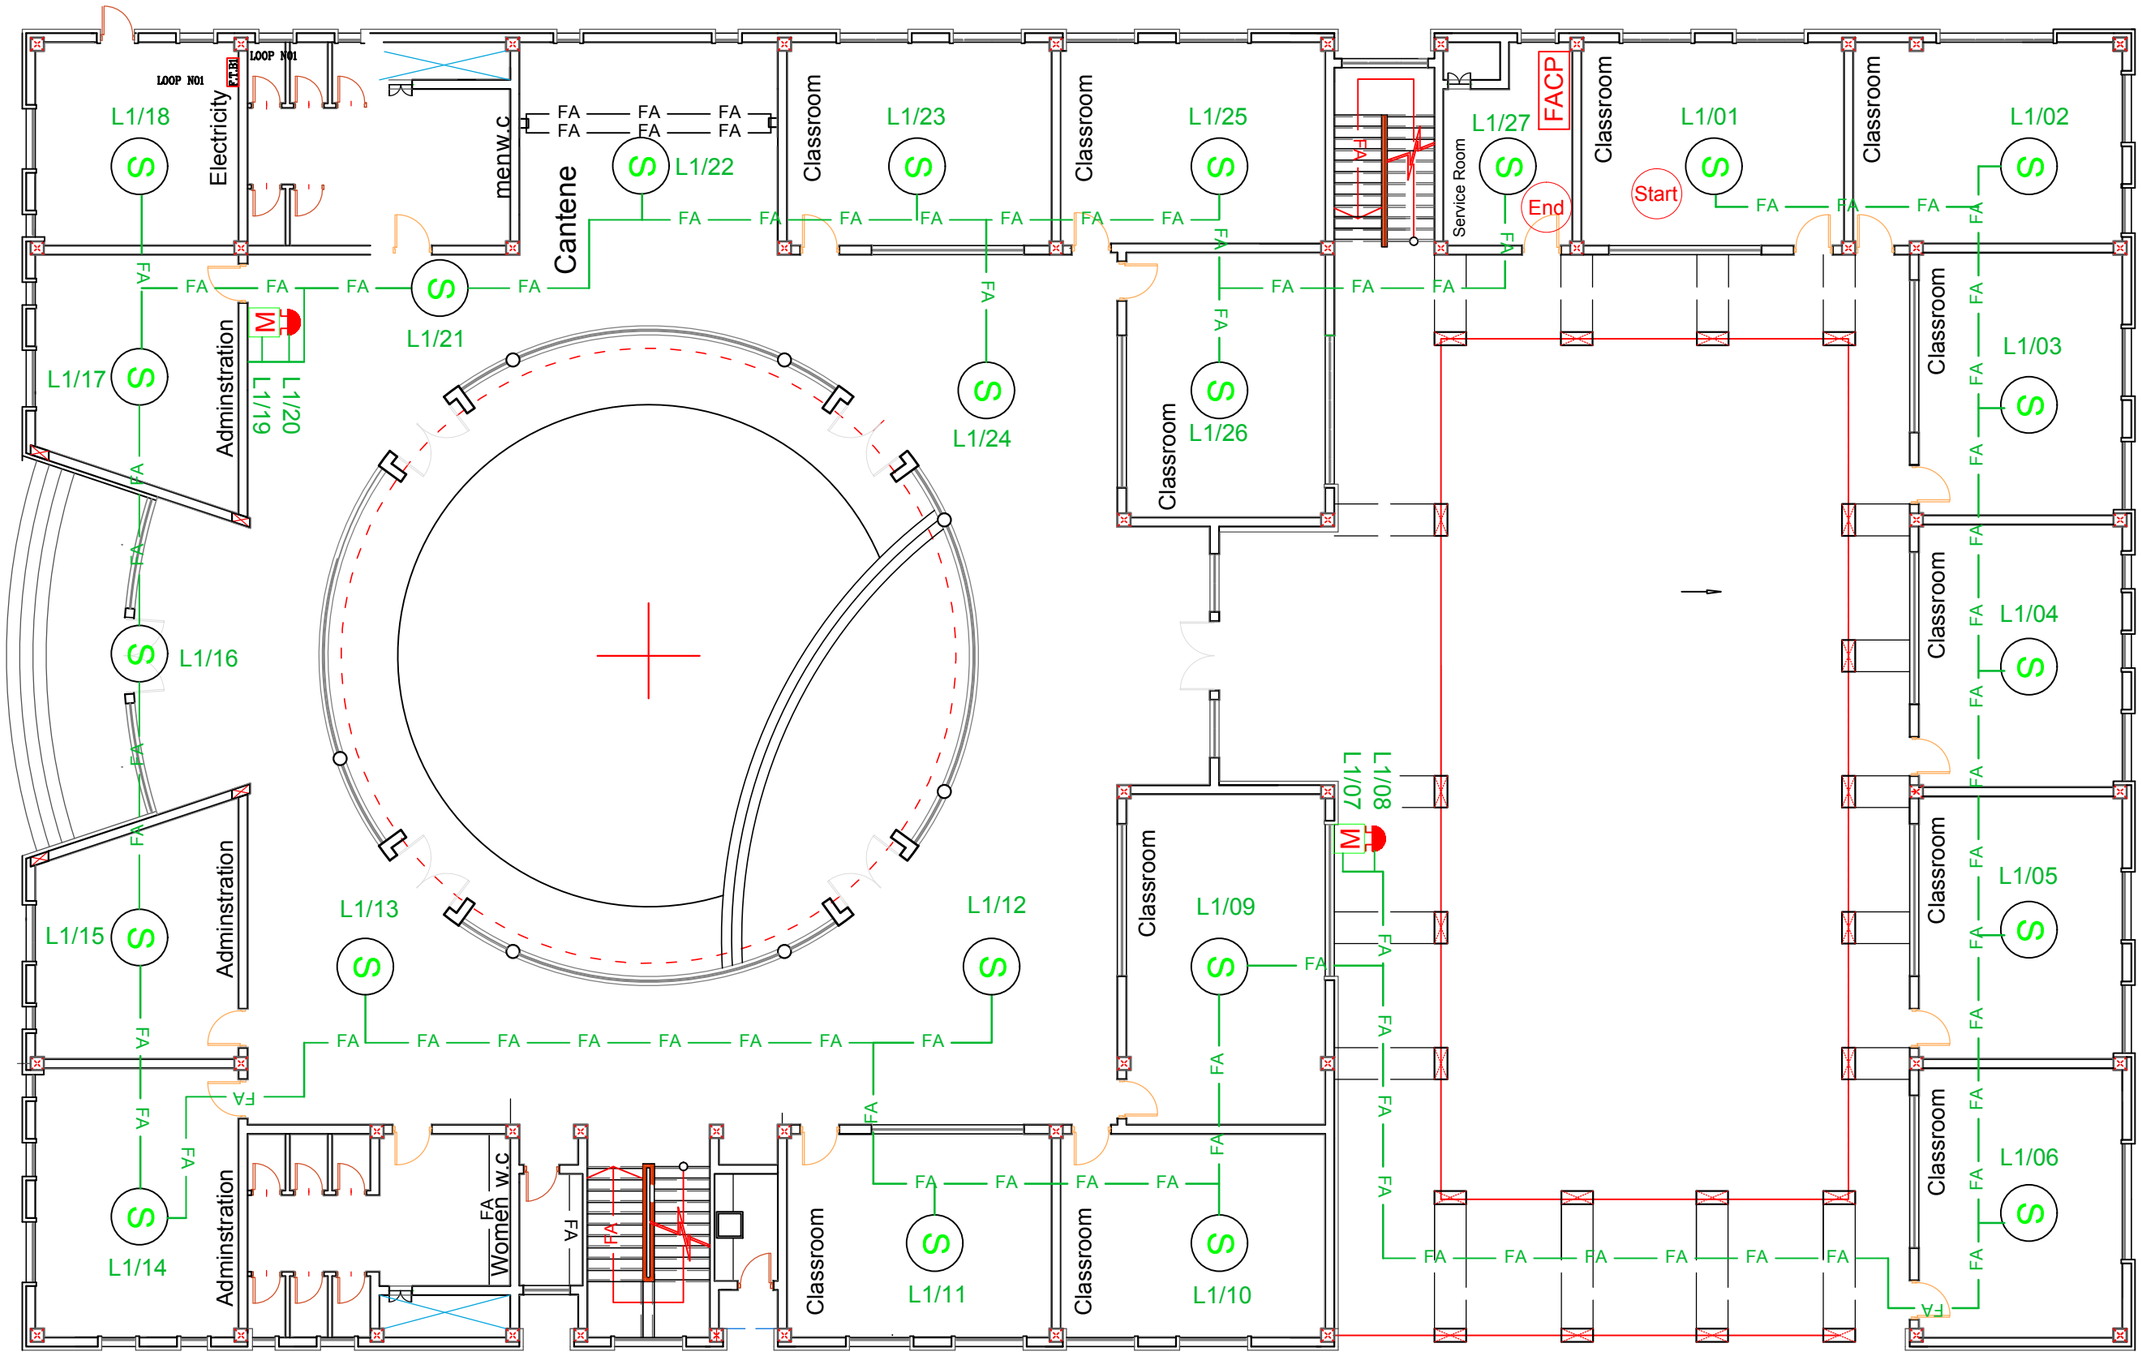

Legend :

Symbol	Description	NO
S	Ceiling Smoke Detector	23
	Flash+Sounder	2
M	Break Glass	2
FACP	Fire Alarm Contro Panel	
Loop 1 : S1 - G (1- 27)		

ديوان الوقف الشيعي
العتبة العباسية المقدسة
قسم المشاريع الهندسية

اسم المشروع :
مدارس العميد
الحـــر

رسم المهندس :
أحمد قصي

التدقيق الشبكي المهندس :
محمد رعد

تصميم المهندس :
حيدر حميد

تدقيق المهندس :
فراس عباس

مصادقة المهندس :
ضياء مجيد الصائغ

اسم المخطط :
منظومة
اطفاء الحريق

عنوان المخطط :
مخططات بناية المدرسة ١
الطابق الارضي

Layout No.	29
Revision	2
Date	19/08/2022
Draw Scale	1\1

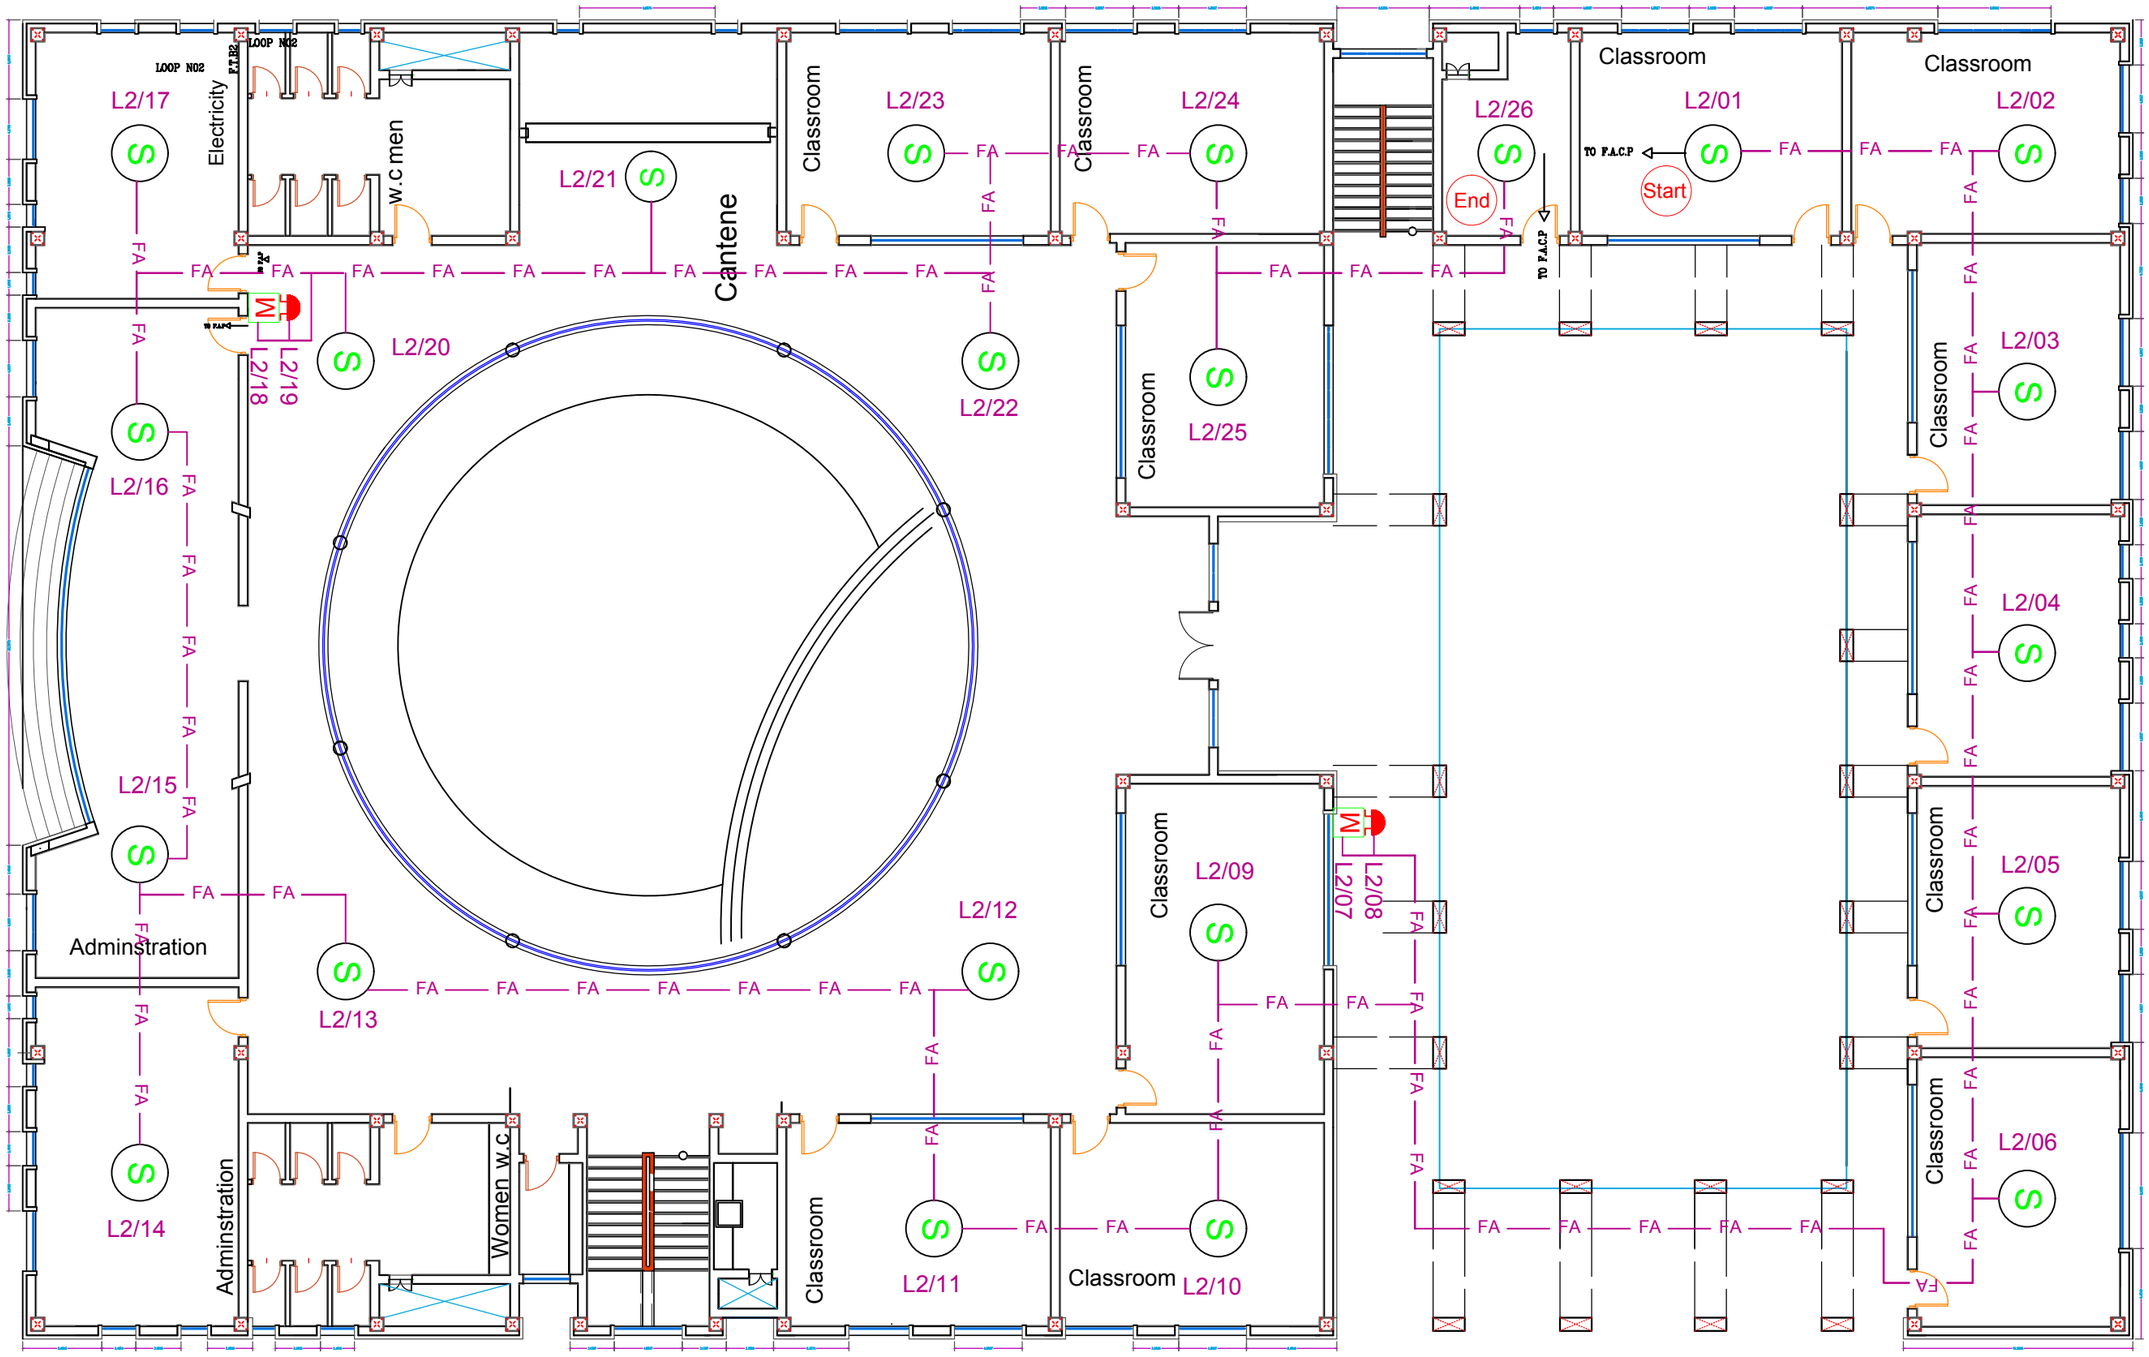

Legend :

Symbol	Description	NO
S	Ceiling Smoke Detector	22
	Flash+Sounder	2
M	Break Glass	2
FACP	Fire Alarm Contro Panel	
Loop 2 : S1 - F1 (1- 26)		

ديوان الوقف الشيعي
العتبة العباسية المقدسة
قسم المشاريع الهندسية

اسم المشروع :
مدارس العميد
الحـــر

رسم المهندس :
أحمد قصي

التدقيق الشبكي المهندس :
محمد رعد

تصميم المهندس :
حيدر حميد

تدقيق المهندس :
فراس عباس

مصادقة المهندس :
ضياء مجيد الصائغ

اسم المخطط :
منظومة
اطفاء الحريق

عنوان المخطط :
مخططات بناية المدرسة ١
الطابق الاول

Layout No.	30
Revision	2
Date	19/07/2022
Draw Scale	1\1

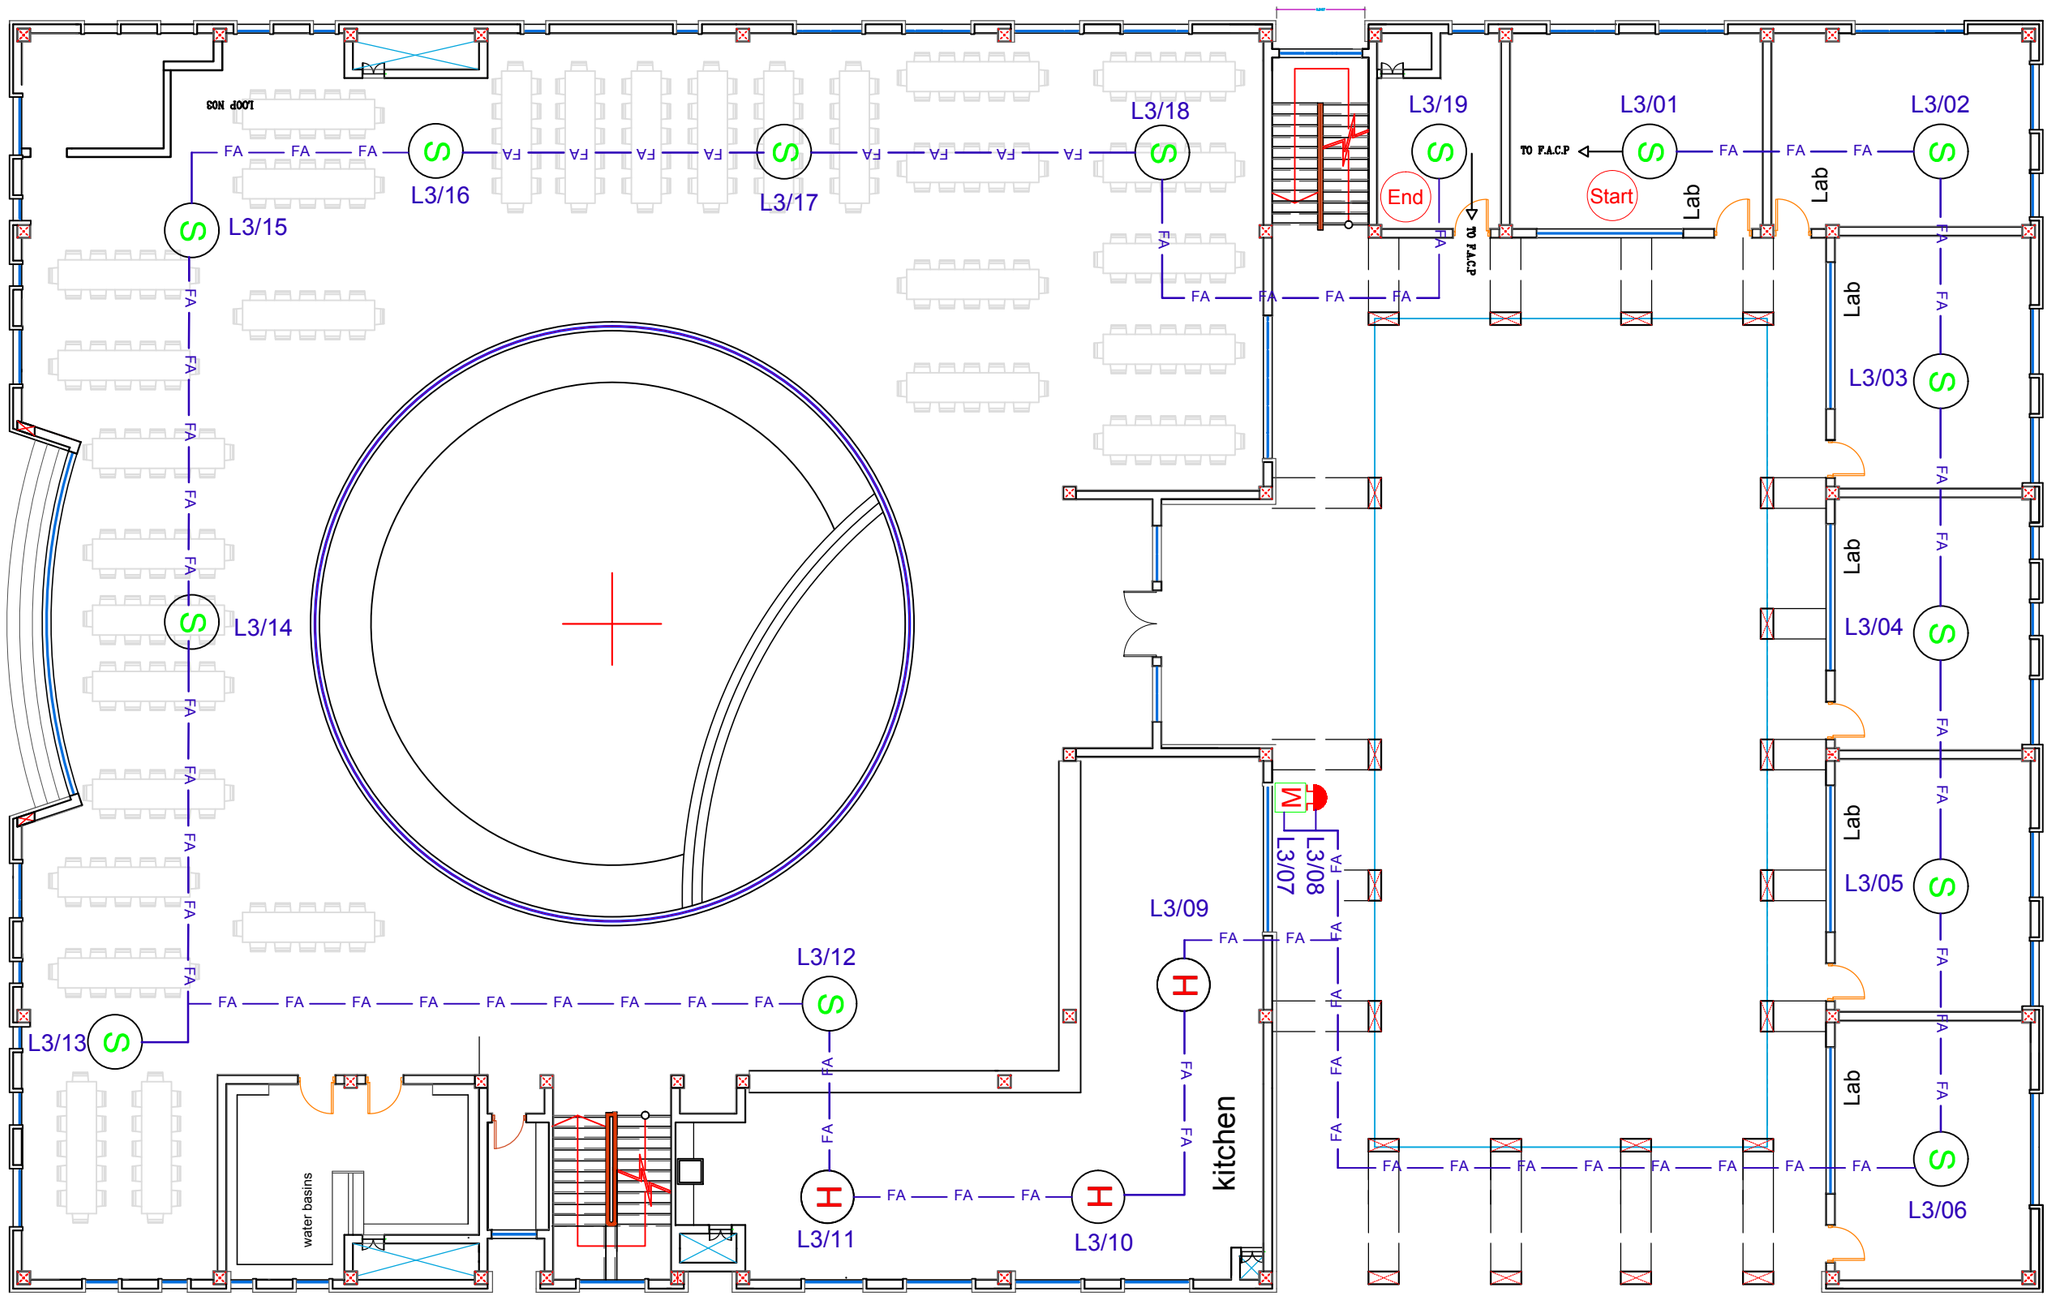

Legend :

Symbol	Description	NO
S	Ceiling Smoke Detector	14
H	Ceiling Multi (Smoke , Gass And Heat) Detector	3
	Flash+Sounder	1
M	Break Glass	1
FACP	Fire Alarm Contro Panel	
Loop 3 : S1 - F2 (1- 19)		

ديوان الوقف الشيعي
العتبة العباسية المقدسة
قسم المشاريع الهندسية

اسم المشروع :
مدارس العميد
الحـــر

رسم المهندس :
أحمد قصي

التدقيق الشبكي المهندس :
محمد رعد

تصميم المهندس :
حيدر حميد

تدقيق المهندس :
فراس عباس

مصادقة المهندس :
ضياء مجيد الصائغ

اسم المخطط :
منظومة
اطفاء الحريق

عنوان المخطط :
مخططات بناية المدرسة ١
الطابق الثاني

Layout No.	31
Revision	2
Date	20/08/2022
Draw Scale	1\1

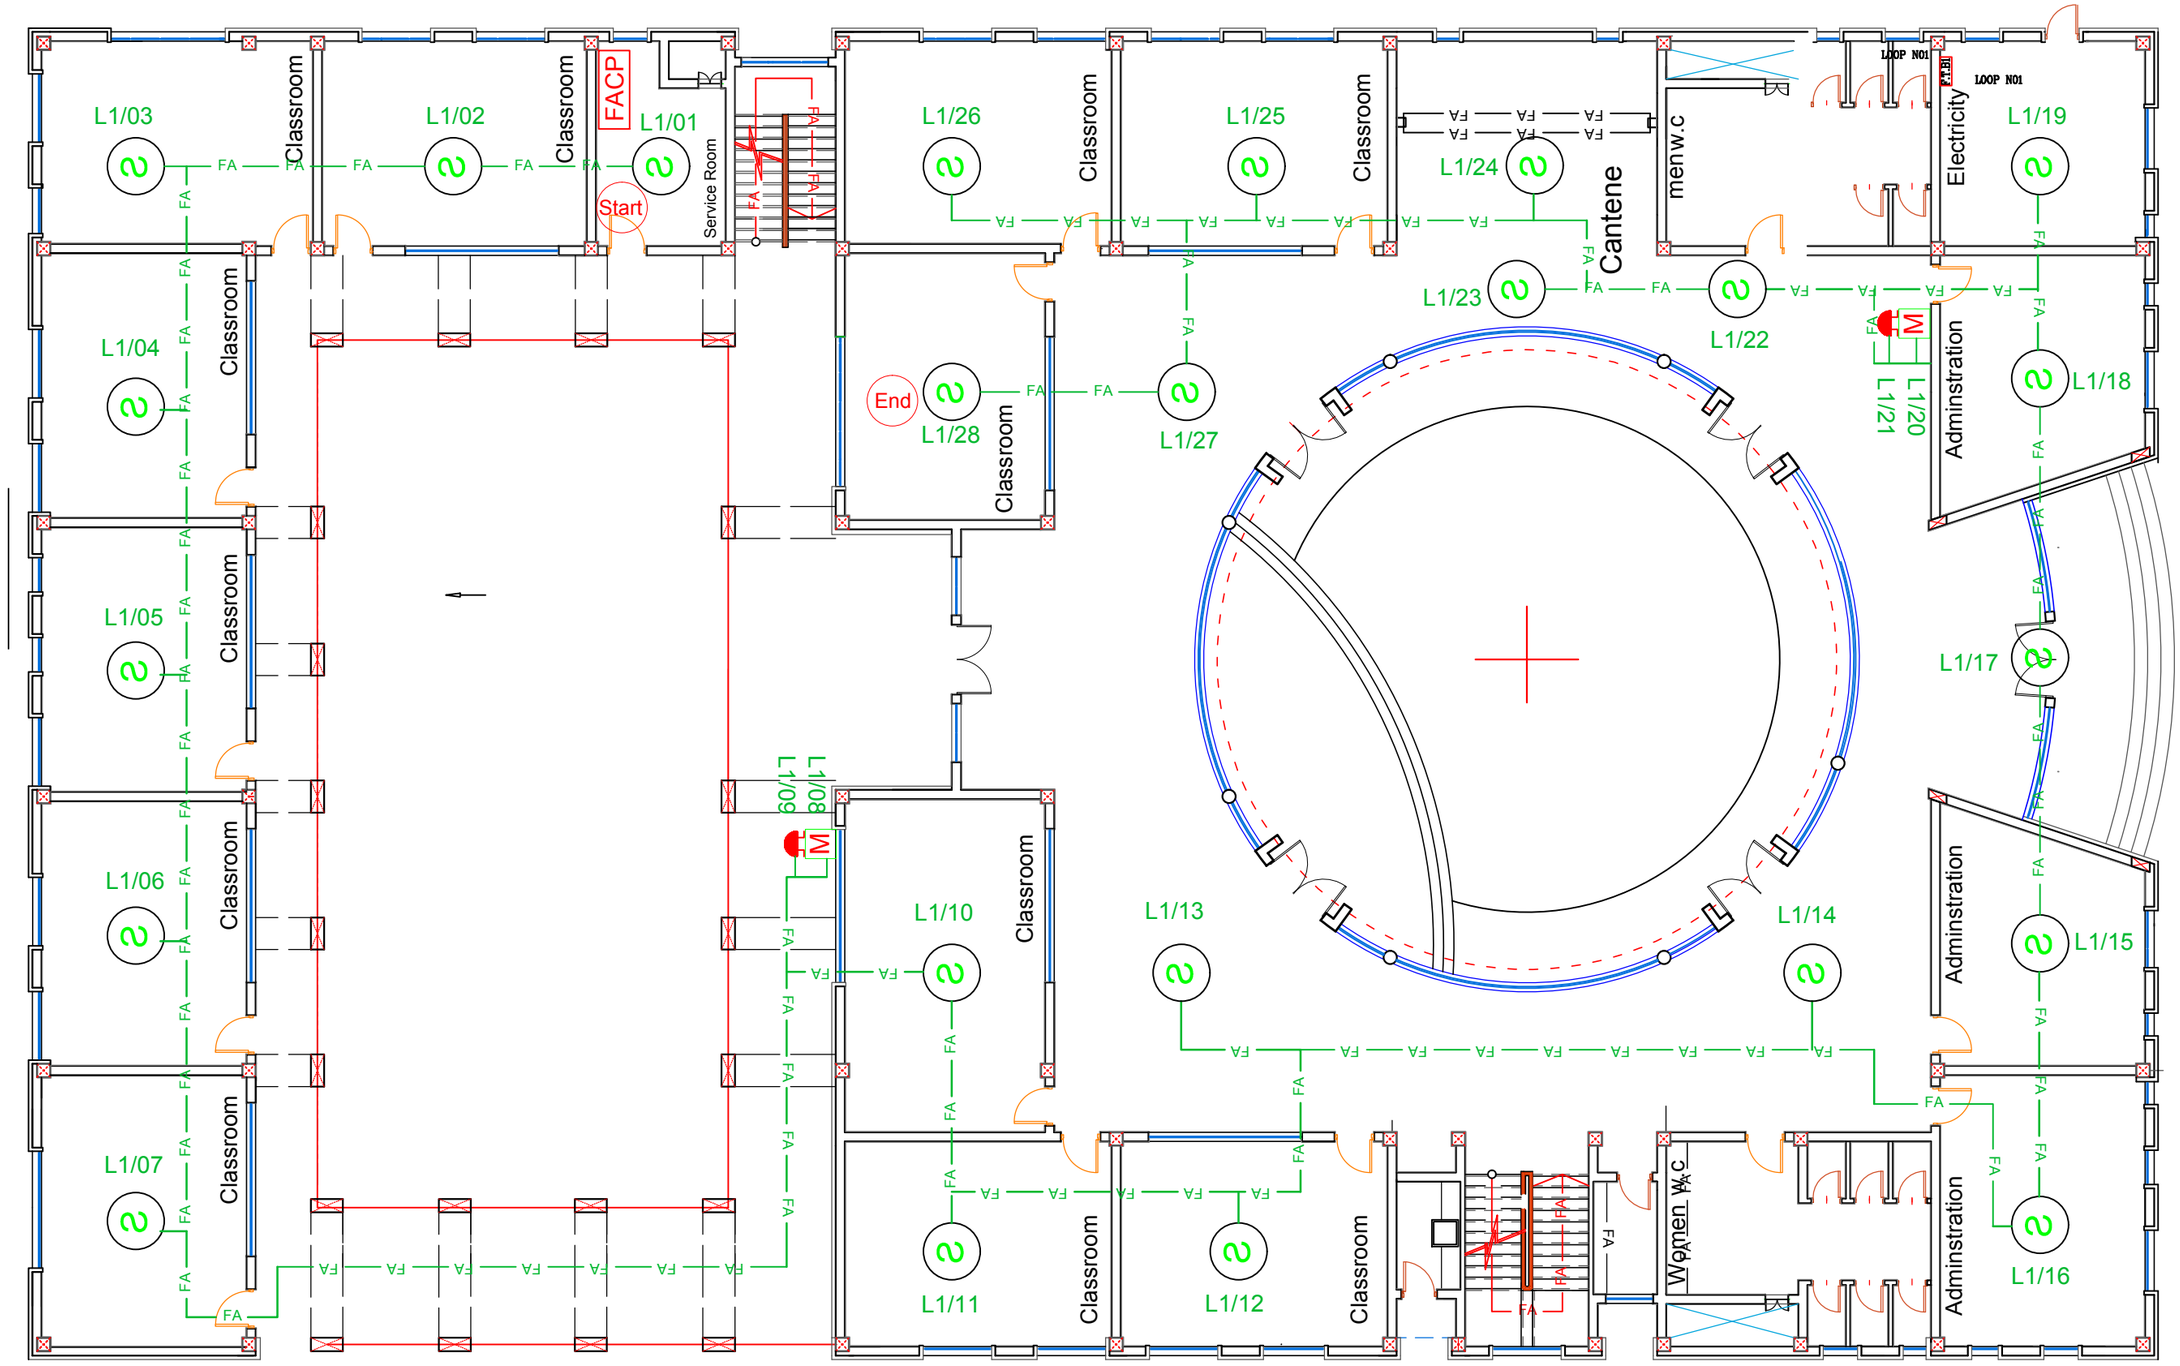

Legend :

Symbol	Description	NO
S	Ceiling Smoke Detector	24
	Flash+Sounder	2
M	Break Glass	2
FACP	Fire Alarm Contro Panel	
Loop 1 : S2 - G (1- 28)		

ديوان الوقف الشيعي
العتبة العباسية المقدسة
قسم المشاريع الهندسية

اسم المشروع :
مدارس العميد
الحـــر

رسم المهندس :
أحمد قصي

التدقيق الشبكي المهندس :
محمد رعد

تصميم المهندس :
حيدر حميد

تدقيق المهندس :
فراس عباس

مصادقة المهندس :
ضياء مجيد الصائغ

اسم المخطط :
منظومة
اطفاء الحريق

عنوان المخطط :
مخططات بناية المدرسة ٢
الطابق الارضي

Layout No.	32
Revision	2
Date	20/08/2022
Draw Scale	1\1

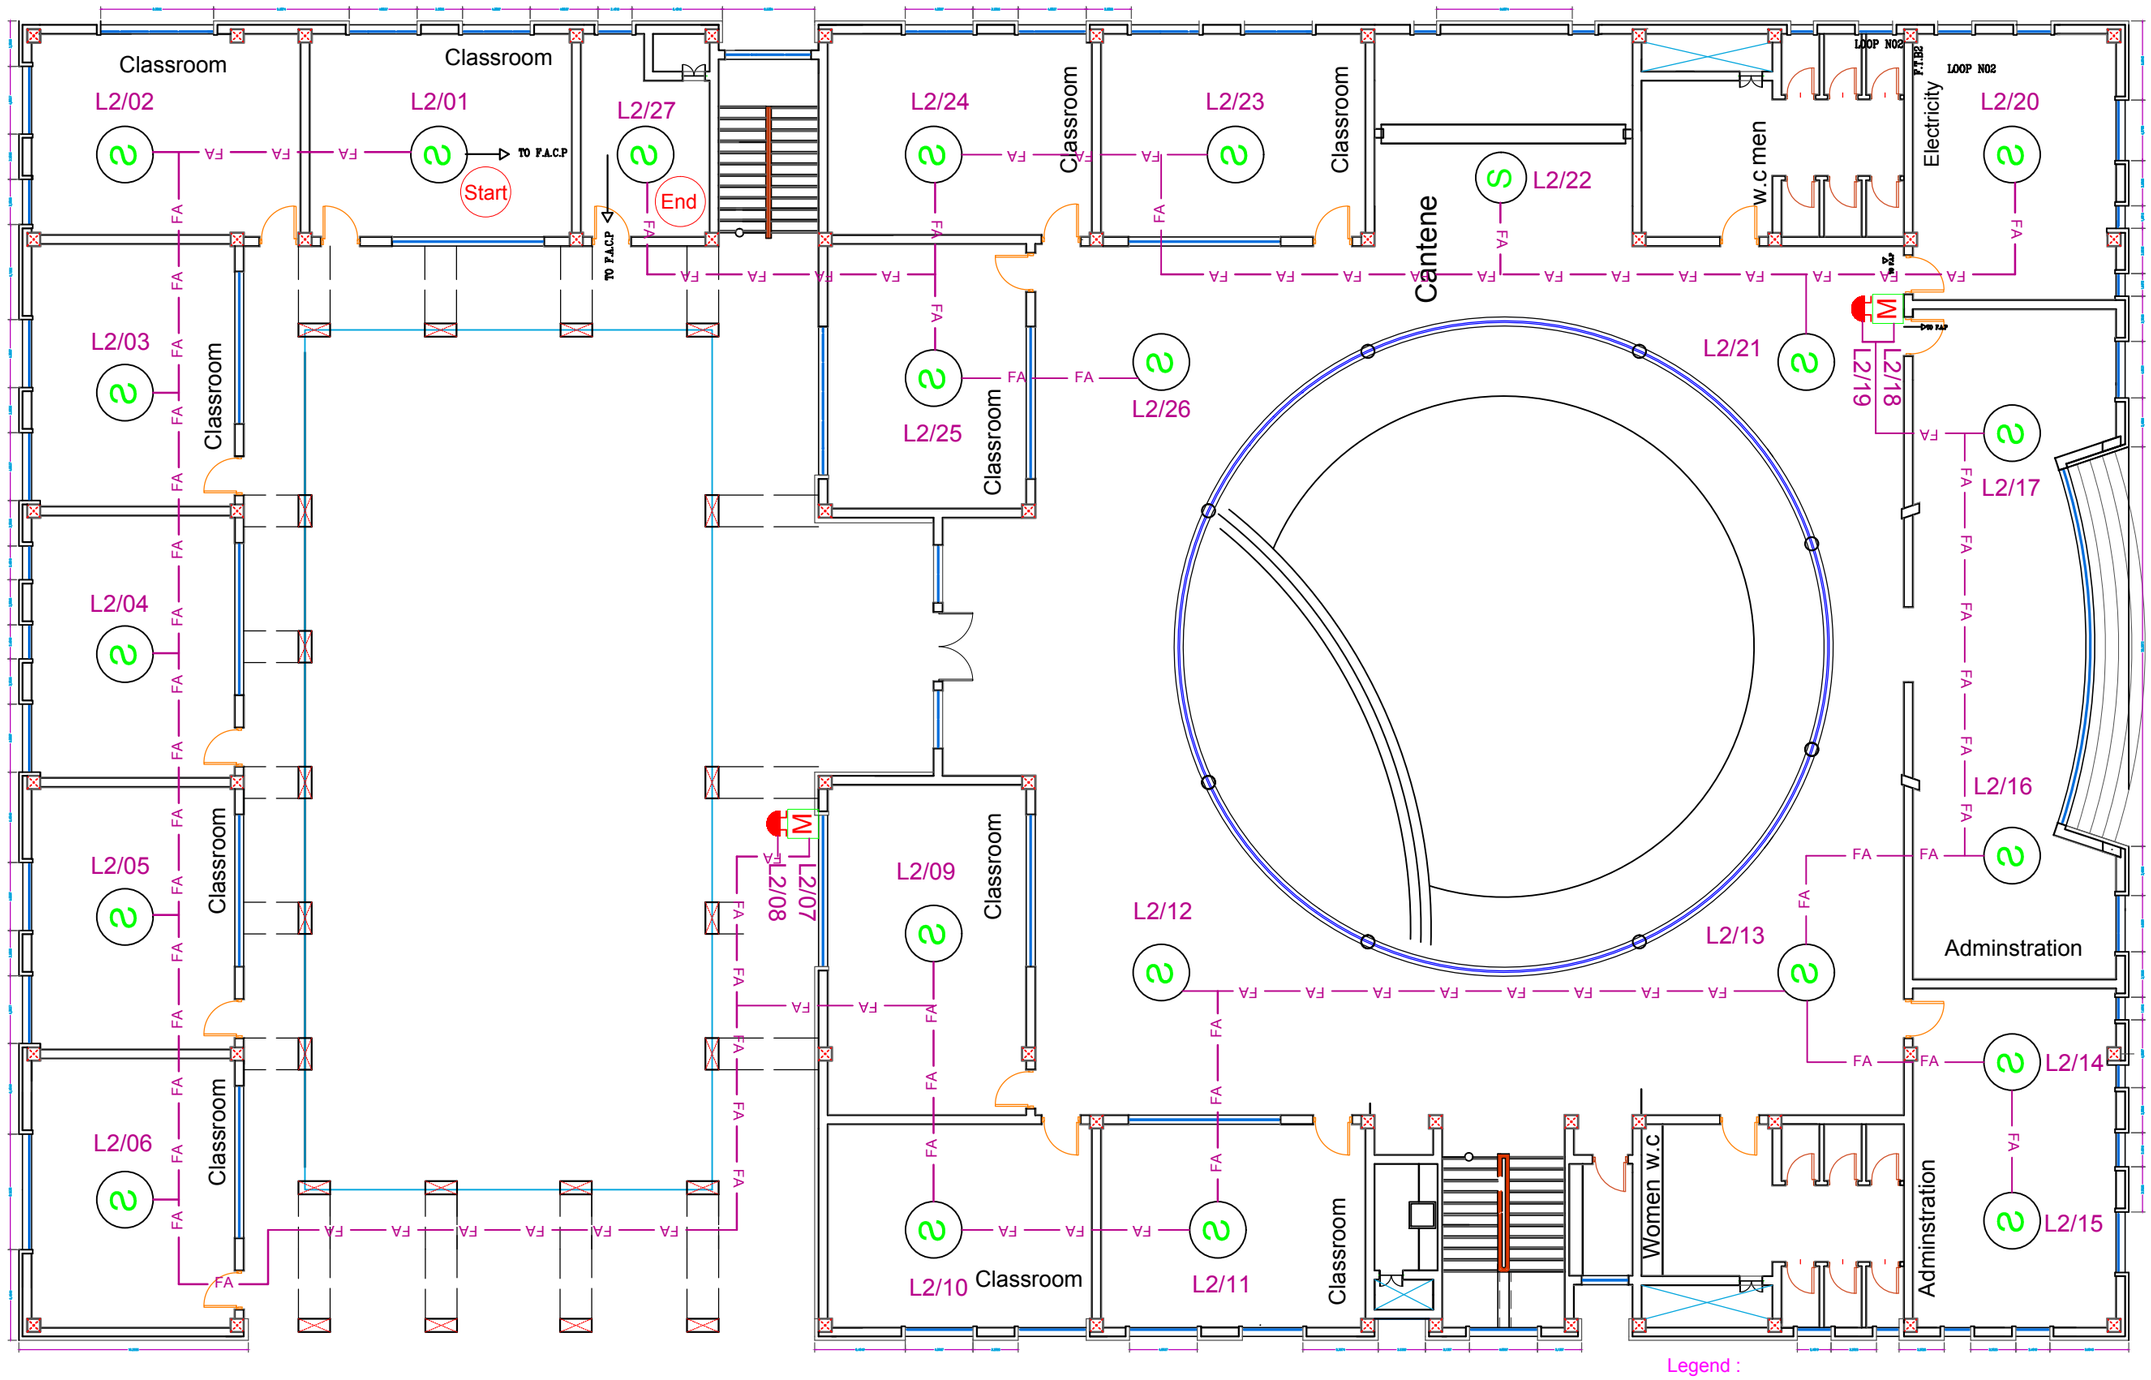

Legend :

Symbol	Description	NO
S	Ceiling Smoke Detector	23
	Flash+Sounder	2
M	Break Glass	2
FACP	Fire Alarm Contro Panel	
Loop 2 : S2 - F1 (1- 27)		

ديوان الوقف الشيعي
العتبة العباسية المقدسة
قسم المشاريع الهندسية

اسم المشروع :
مدارس العميد
الحـــر

رسم المهندس :
أحمد قصي

التدقيق الشبكي المهندس :
محمد رعد

تصميم المهندس :
حيدر حميد

تدقيق المهندس :
فراس عباس

مصادقة المهندس :
ضياء مجيد الصائغ

اسم المخطط :
منظومة
اطفاء الحريق

عنوان المخطط :
مخططات بناية المدرسة ٢
الطابق الاول

Layout No.	33
Revision	2
Date	20/08/2022
Draw Scale	1\1

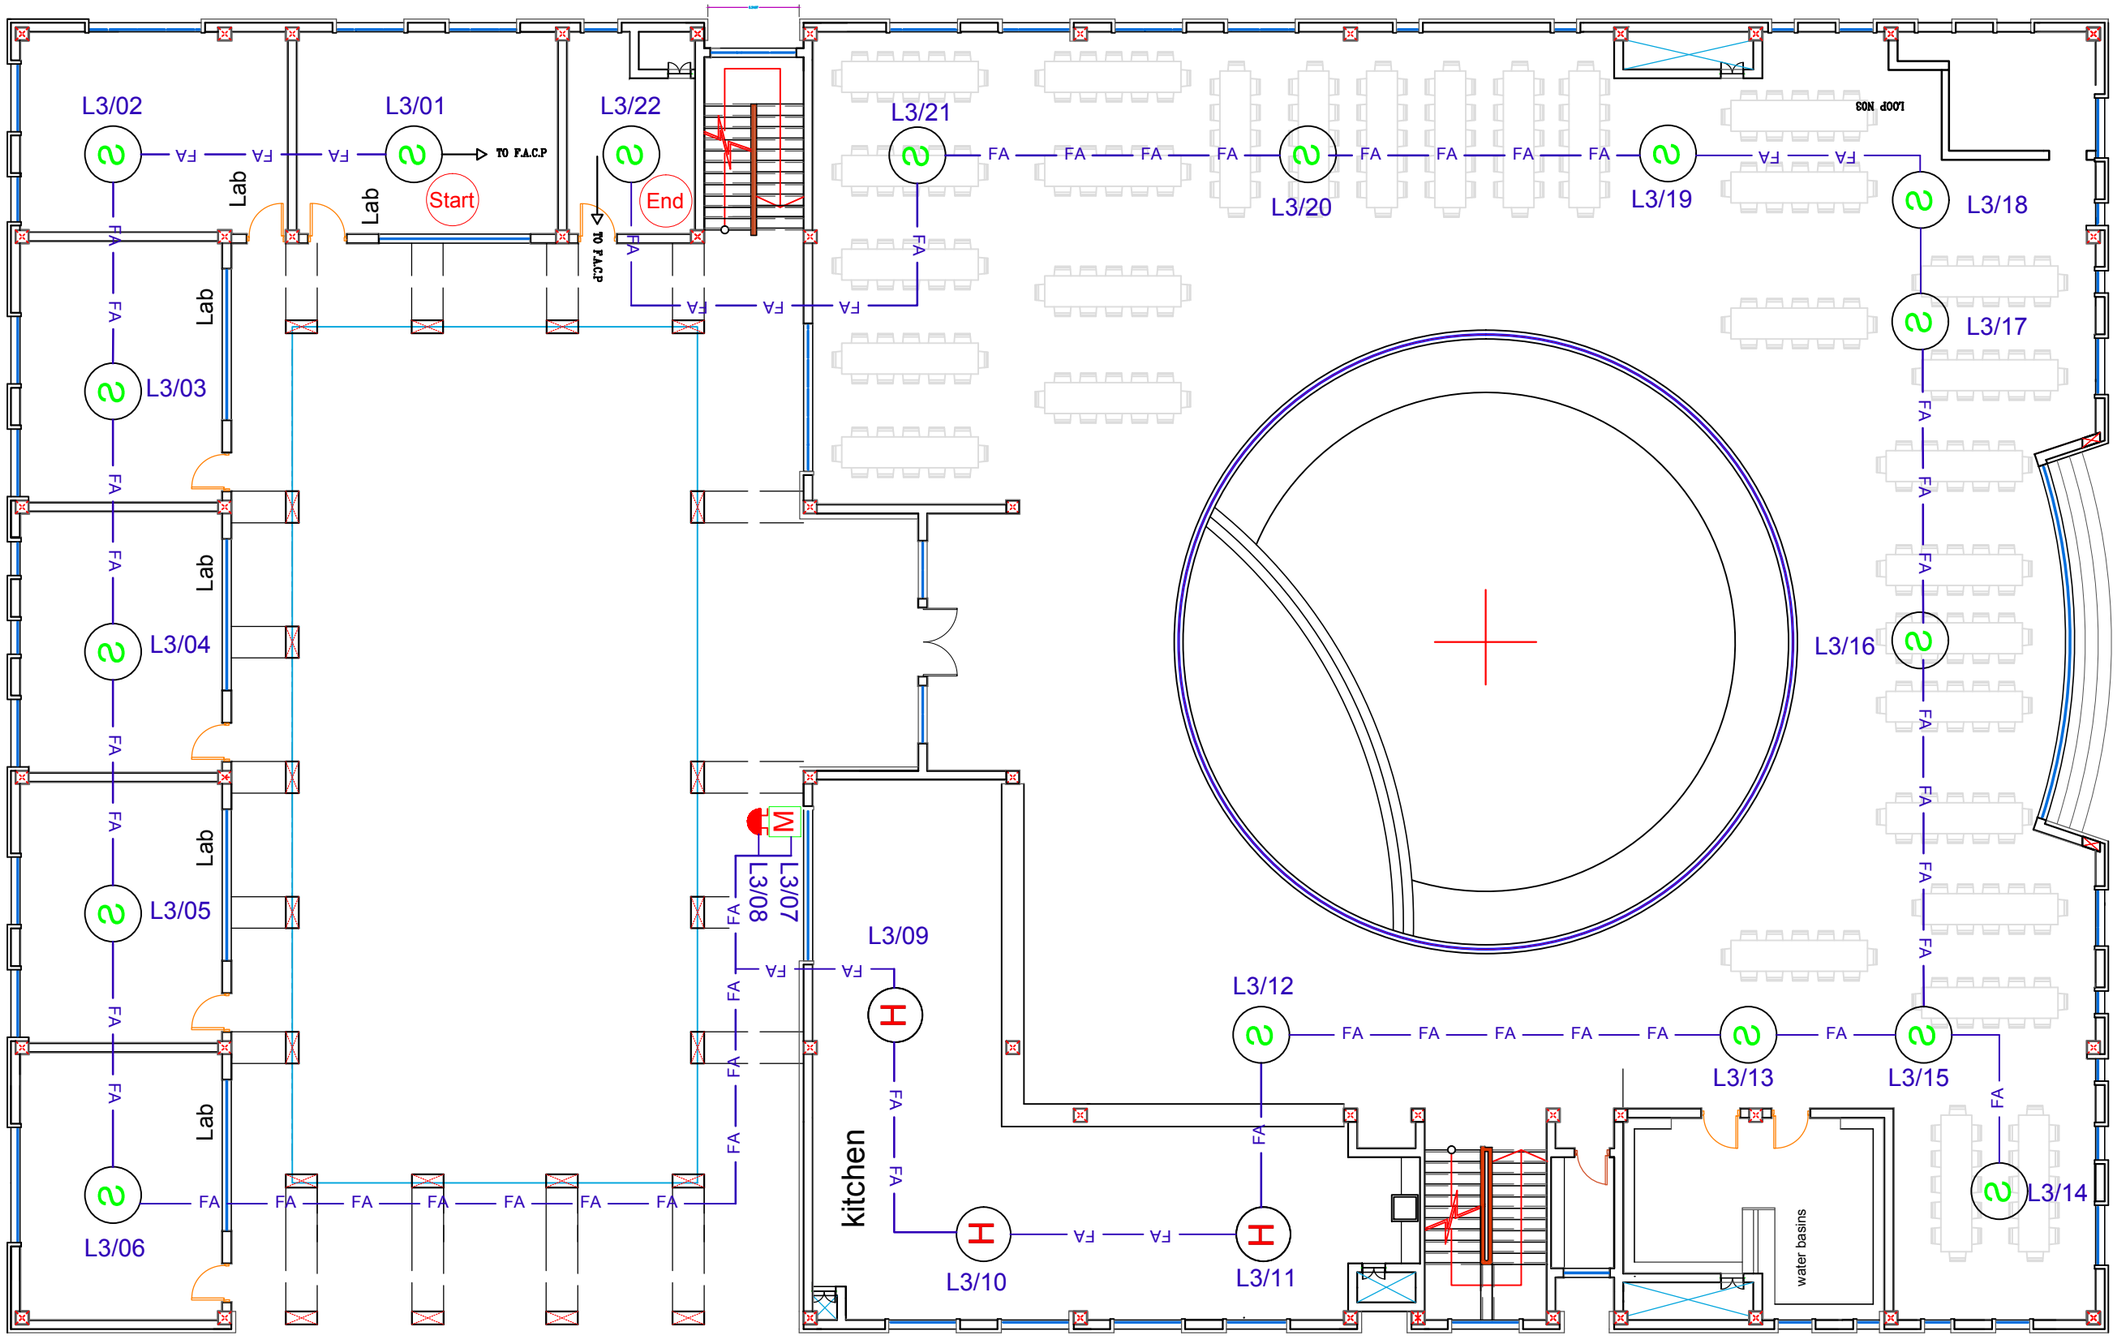

Legend :

Symbol	Description	NO
S	Ceiling Smoke Detector	17
H	Ceiling Multi (Smoke , Gass And Heat) Detector	3
	Flash+Sounder	1
M	Break Glass	1
FACP	Fire Alarm Contro Panel	
	Loop 3 : S2 - F2 (1- 22)	

ديوان الوقف الشيعي
العتبة العباسية المقدسة
قسم المشاريع الهندسية

اسم المشروع :
مدارس العميد
الحـــر

رسم المهندس :
أحمد قصي

التدقيق الشبكي المهندس :
محمد رعد

تصميم المهندس :
حيدر حميد

تدقيق المهندس :
فراس عباس

مصادقة المهندس :
ضياء مجيد الصائغ

اسم المخطط :
منظومة
اطفاء الحريق

عنوان المخطط :
مخططات بناية المدرسة ٢
الطابق الثاني

Layout No.	34
Revision	2
Date	20/08/2022
Draw Scale	1\1

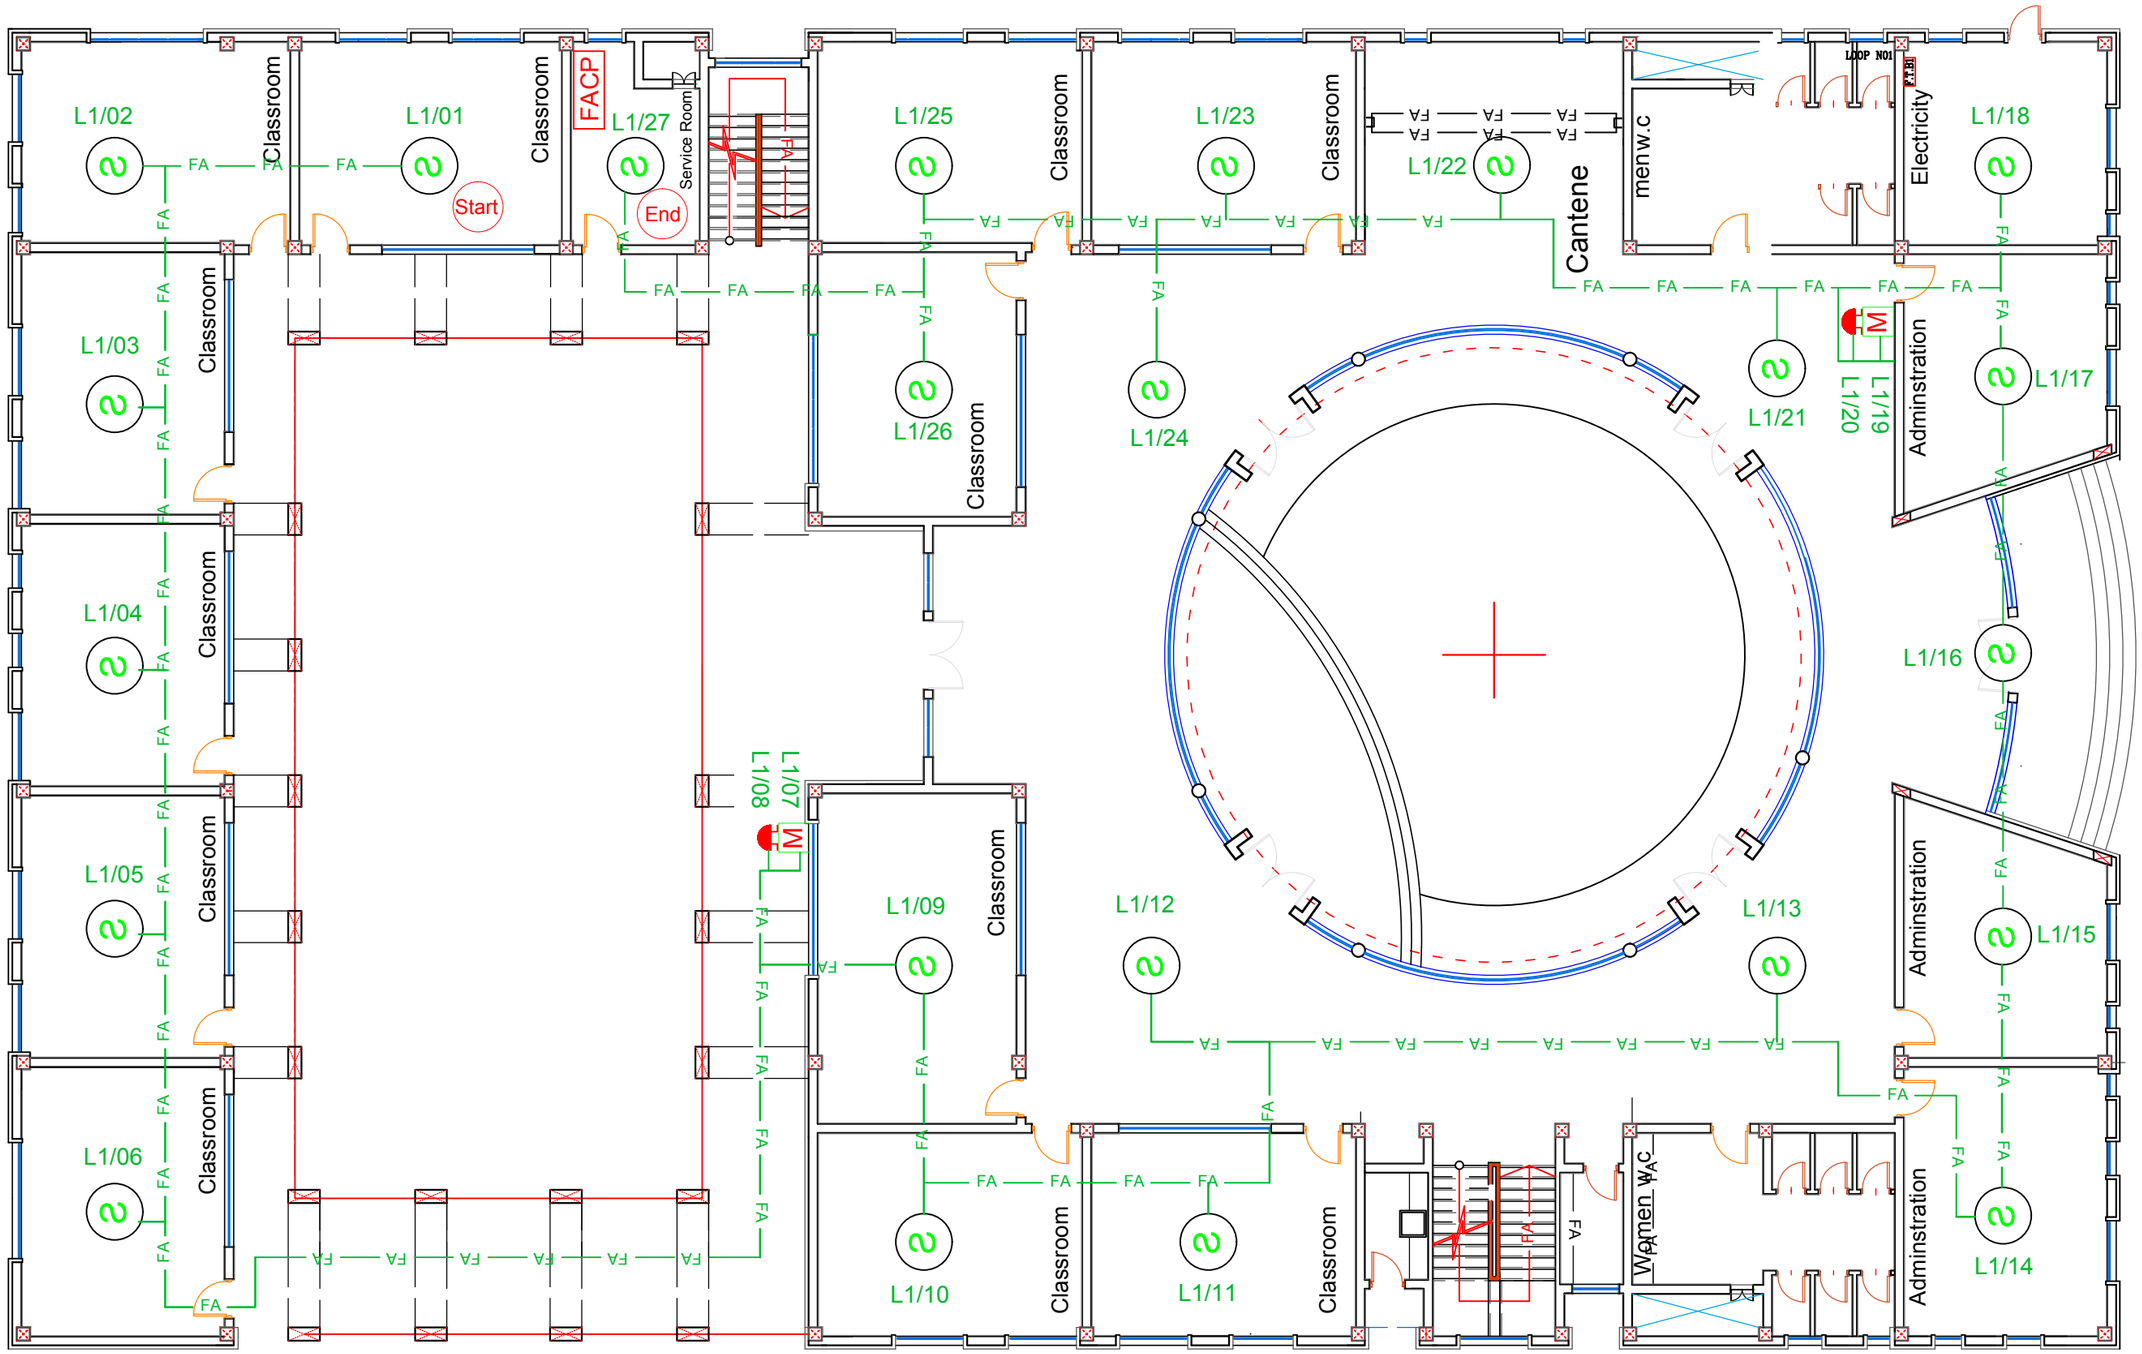

Legend :

Symbol	Description	NO
S	Ceiling Smoke Detector	23
	Flash+Sounder	2
M	Break Glass	2
FACP	Fire Alarm Contro Panel	
Loop 1 : S3 - G (1- 27)		

ديوان الوقف الشيعي
العتبة العباسية المقدسة
قسم المشاريع الهندسية

اسم المشروع :
مدارس العميد
الحـــر

رسم المهندس :
أحمد قصي

التدقيق الشبكي المهندس :
محمد رعد

تصميم المهندس :
حيدر حميد

تدقيق المهندس :
فراس عباس

مصادقة المهندس :
ضياء مجيد الصائغ

اسم المخطط :
منظومة
اطفاء الحريق

عنوان المخطط :
مخططات بناية المدرسة ٣
الطابق الارضي

Layout No.	35
Revision	2
Date	20/08/2022
Draw Scale	1\1

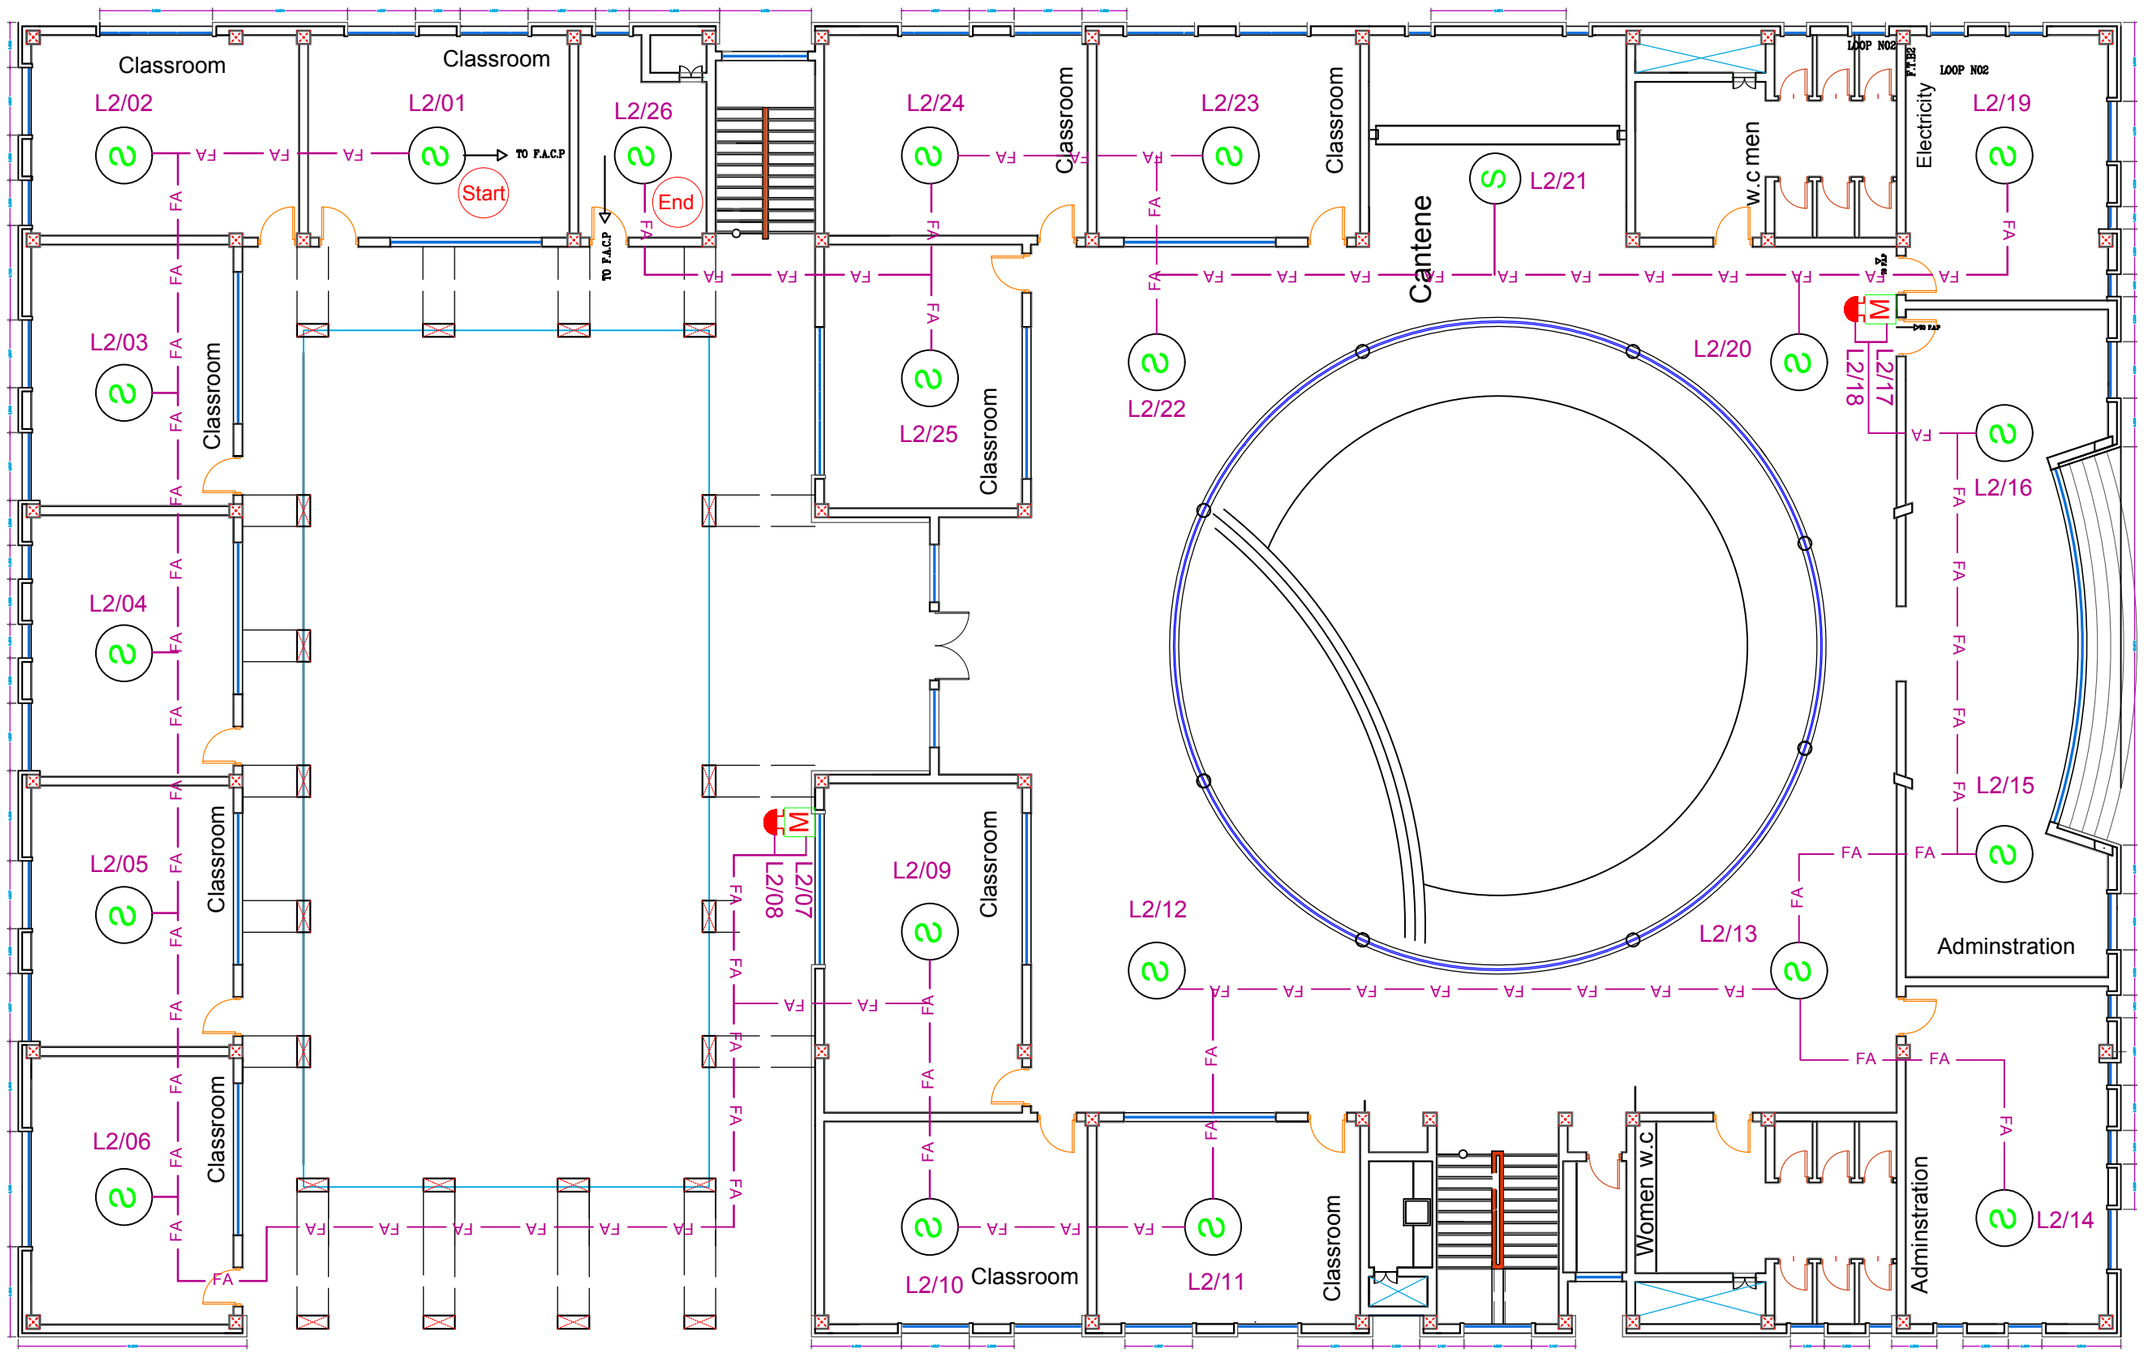

Legend :

Symbol	Description	NO
S	Ceiling Smoke Detector	22
	Flash+Sounder	2
M	Break Glass	2
FACP	Fire Alarm Contro Panel	
Loop 2 : S3 - F1 (1- 26)		

ديوان الوقف الشيعي
العتبة العباسية المقدسة
قسم المشاريع الهندسية

اسم المشروع :
مدارس العميد
الحـــر

رسم المهندس :
أحمد قصي

التدقيق الشبكي المهندس :
محمد رعد

تصميم المهندس :
حيدر حميد

تدقيق المهندس :
فراس عباس

مصادقة المهندس :
ضياء مجيد الصائغ

اسم المخطط :
منظومة
اطفاء الحريق

عنوان المخطط :
مخططات بناية المدرسة ٣
الطابق الاول

Layout No.	36
Revision	2
Date	20/08/2022
Draw Scale	1\1

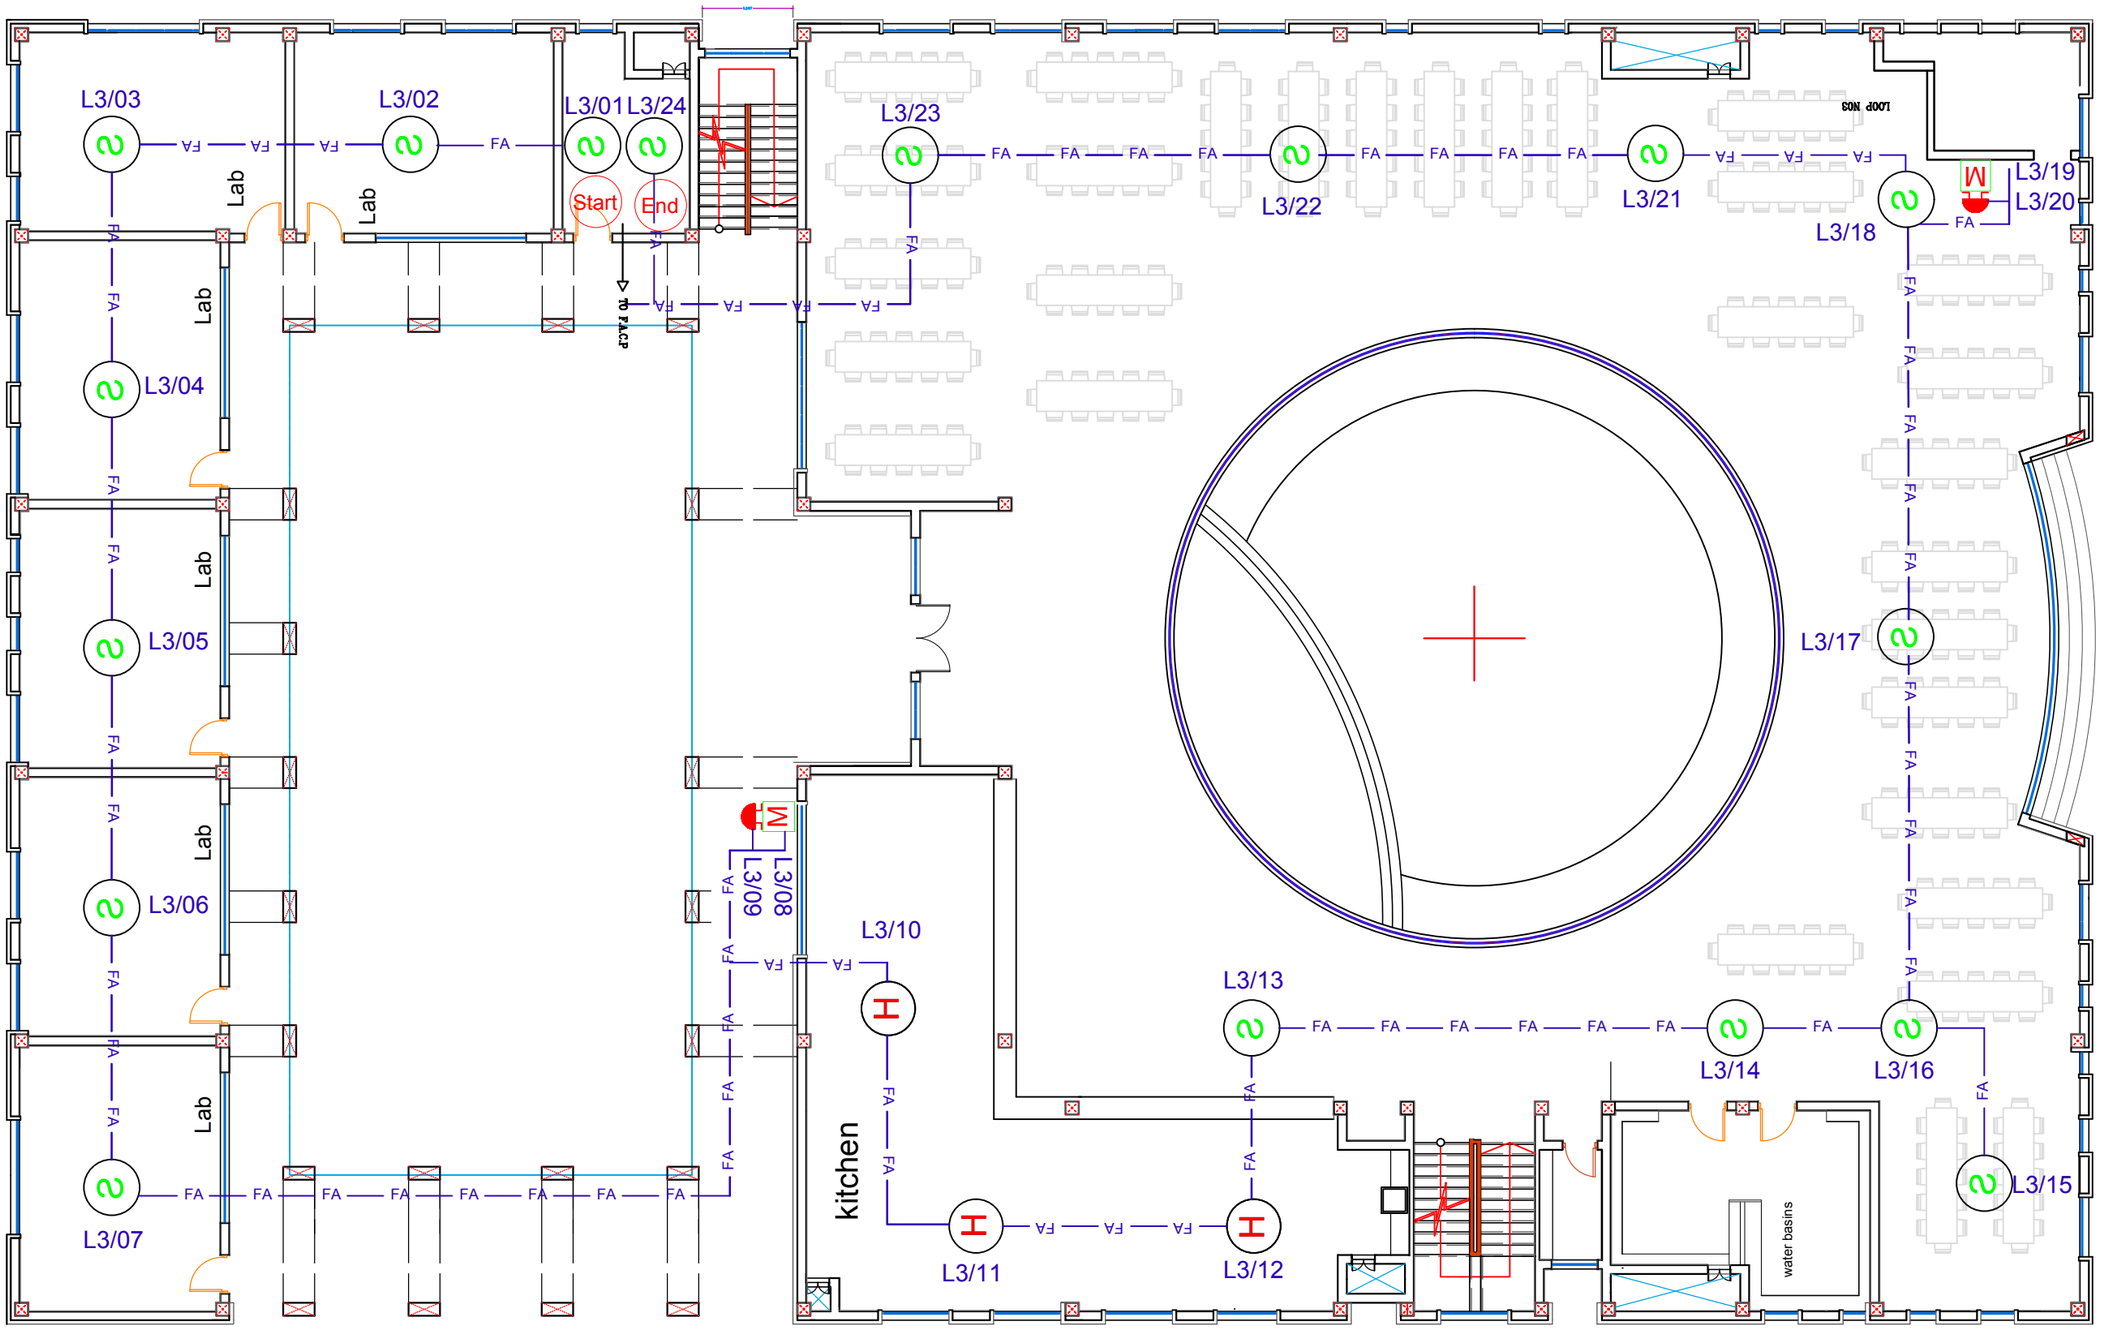

Legend :

Symbol	Description	NO
	Ceiling Smoke Detector	17
	Ceiling Multi (Smoke , Gass And Heat) Detector	3
	Flash+Sounder	2
M	Break Glass	2
FACP	Fire Alarm Contro Panel	
Loop 3 : S3 - F2 (1- 24)		

ديوان الوقف الشيعي
العتبة العباسية المقدسة
قسم المشاريع الهندسية

اسم المشروع :
مدارس العميد
الحـــر

رسم المهندس :
أحمد قصي

التدقيق الشبكي المهندس :
محمد رعد

تصميم المهندس :
حيدر حميد

تدقيق المهندس :
فراس عباس

مصادقة المهندس :
ضياء مجيد الصائغ

اسم المخطط :
منظومة
اطفاء الحريق

عنوان المخطط :
مخططات بناية المدرسة ٣
الطابق الثاني

Layout No.	37
Revision	2
Date	20/08/2022
Draw Scale	1\1